




PROPOSED RESIDENTIAL APARTMENT.
ALONG OSHOGBO STREET, AGUDA,
SURULERE, LAGOS STATE.

FOR
DARALL HOMES LIMITED

FEBRUARY, 2026




O S H O G B O S T R E E T

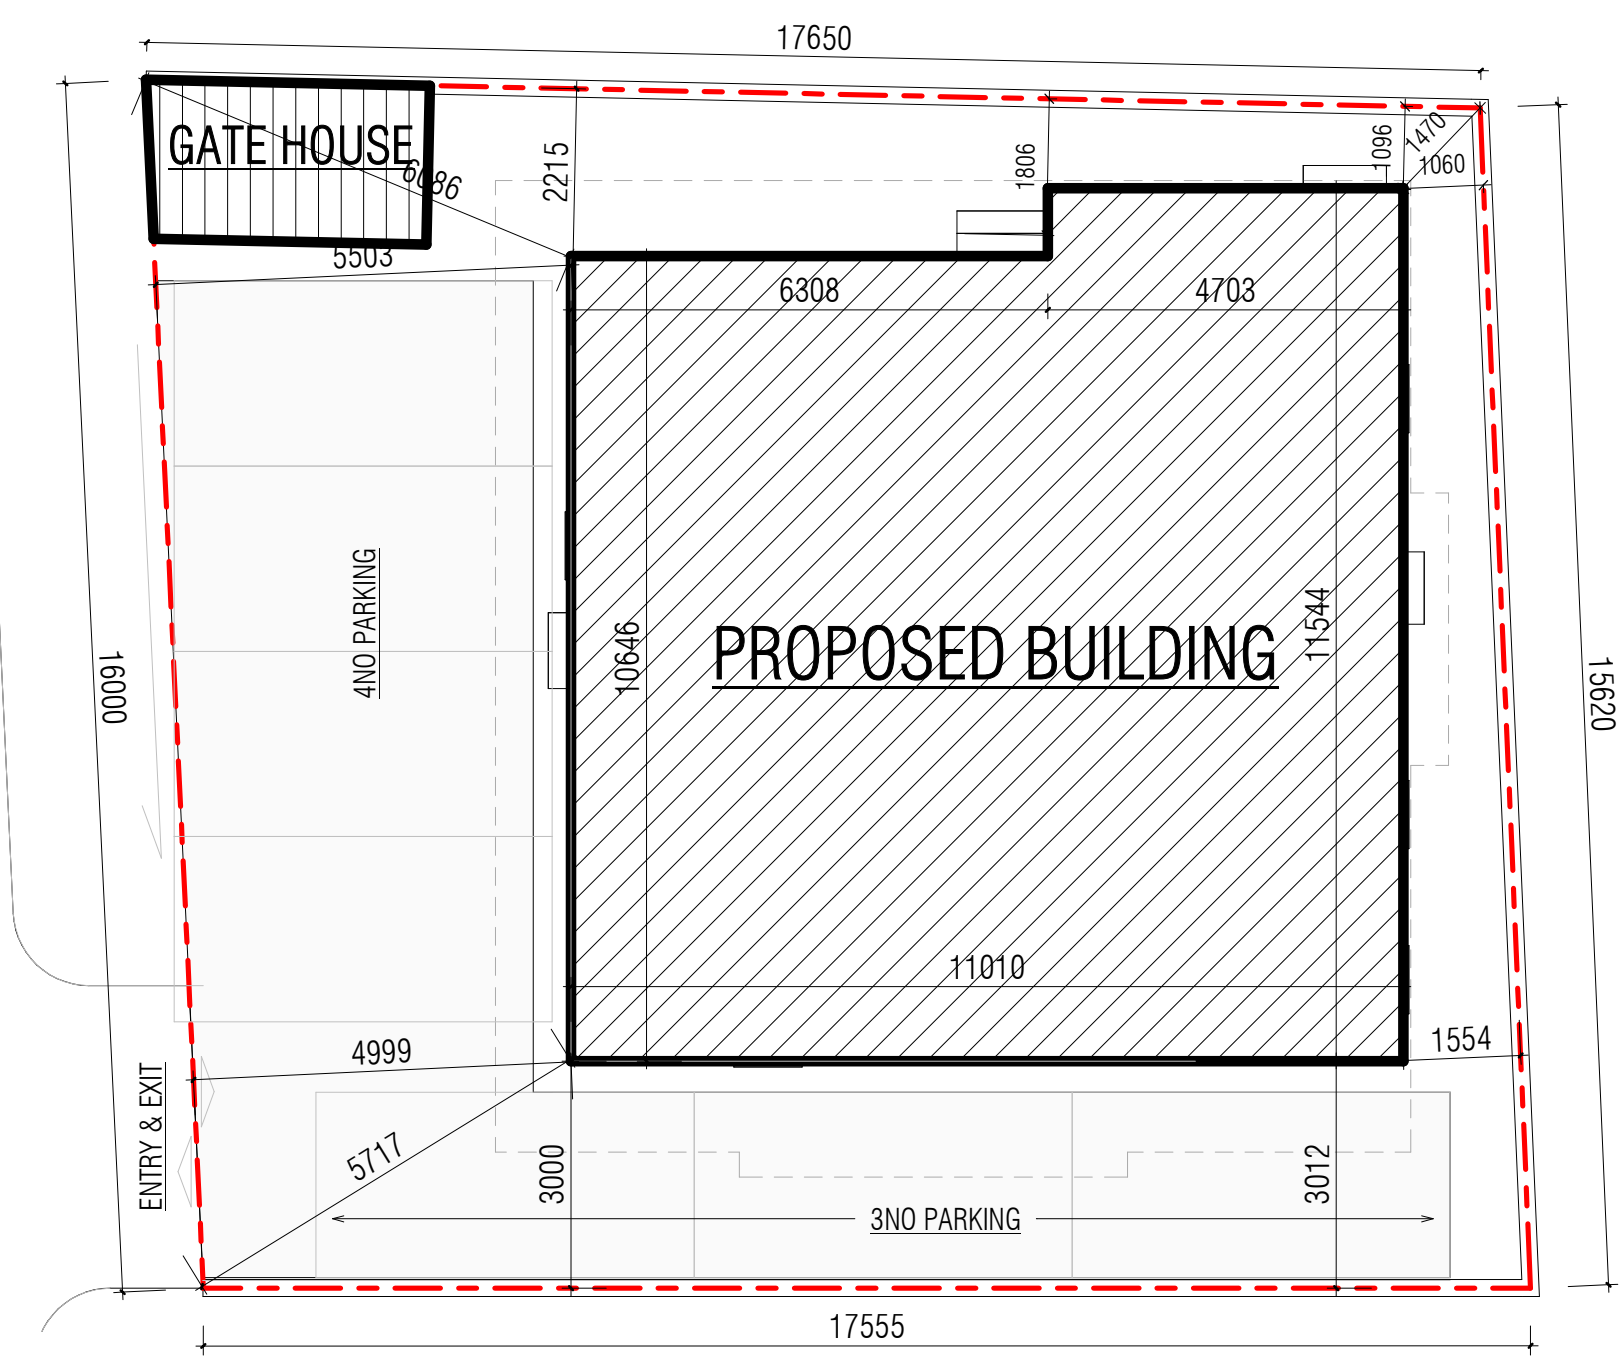

6A, OGUNLEYE STREET, AKOKA, LAGOS.

Project: RESIDENTIAL DEVELOPMENT	Client: DARALL HOMES LIMITED	Status: Approval	
Title: SITE PLAN	Checked By: A.H	Date/Rev: 2/18/2026 9:39:03 AM	Sheet no: P100
Scale/Format: 1 : 100	Drawn By: H.J		

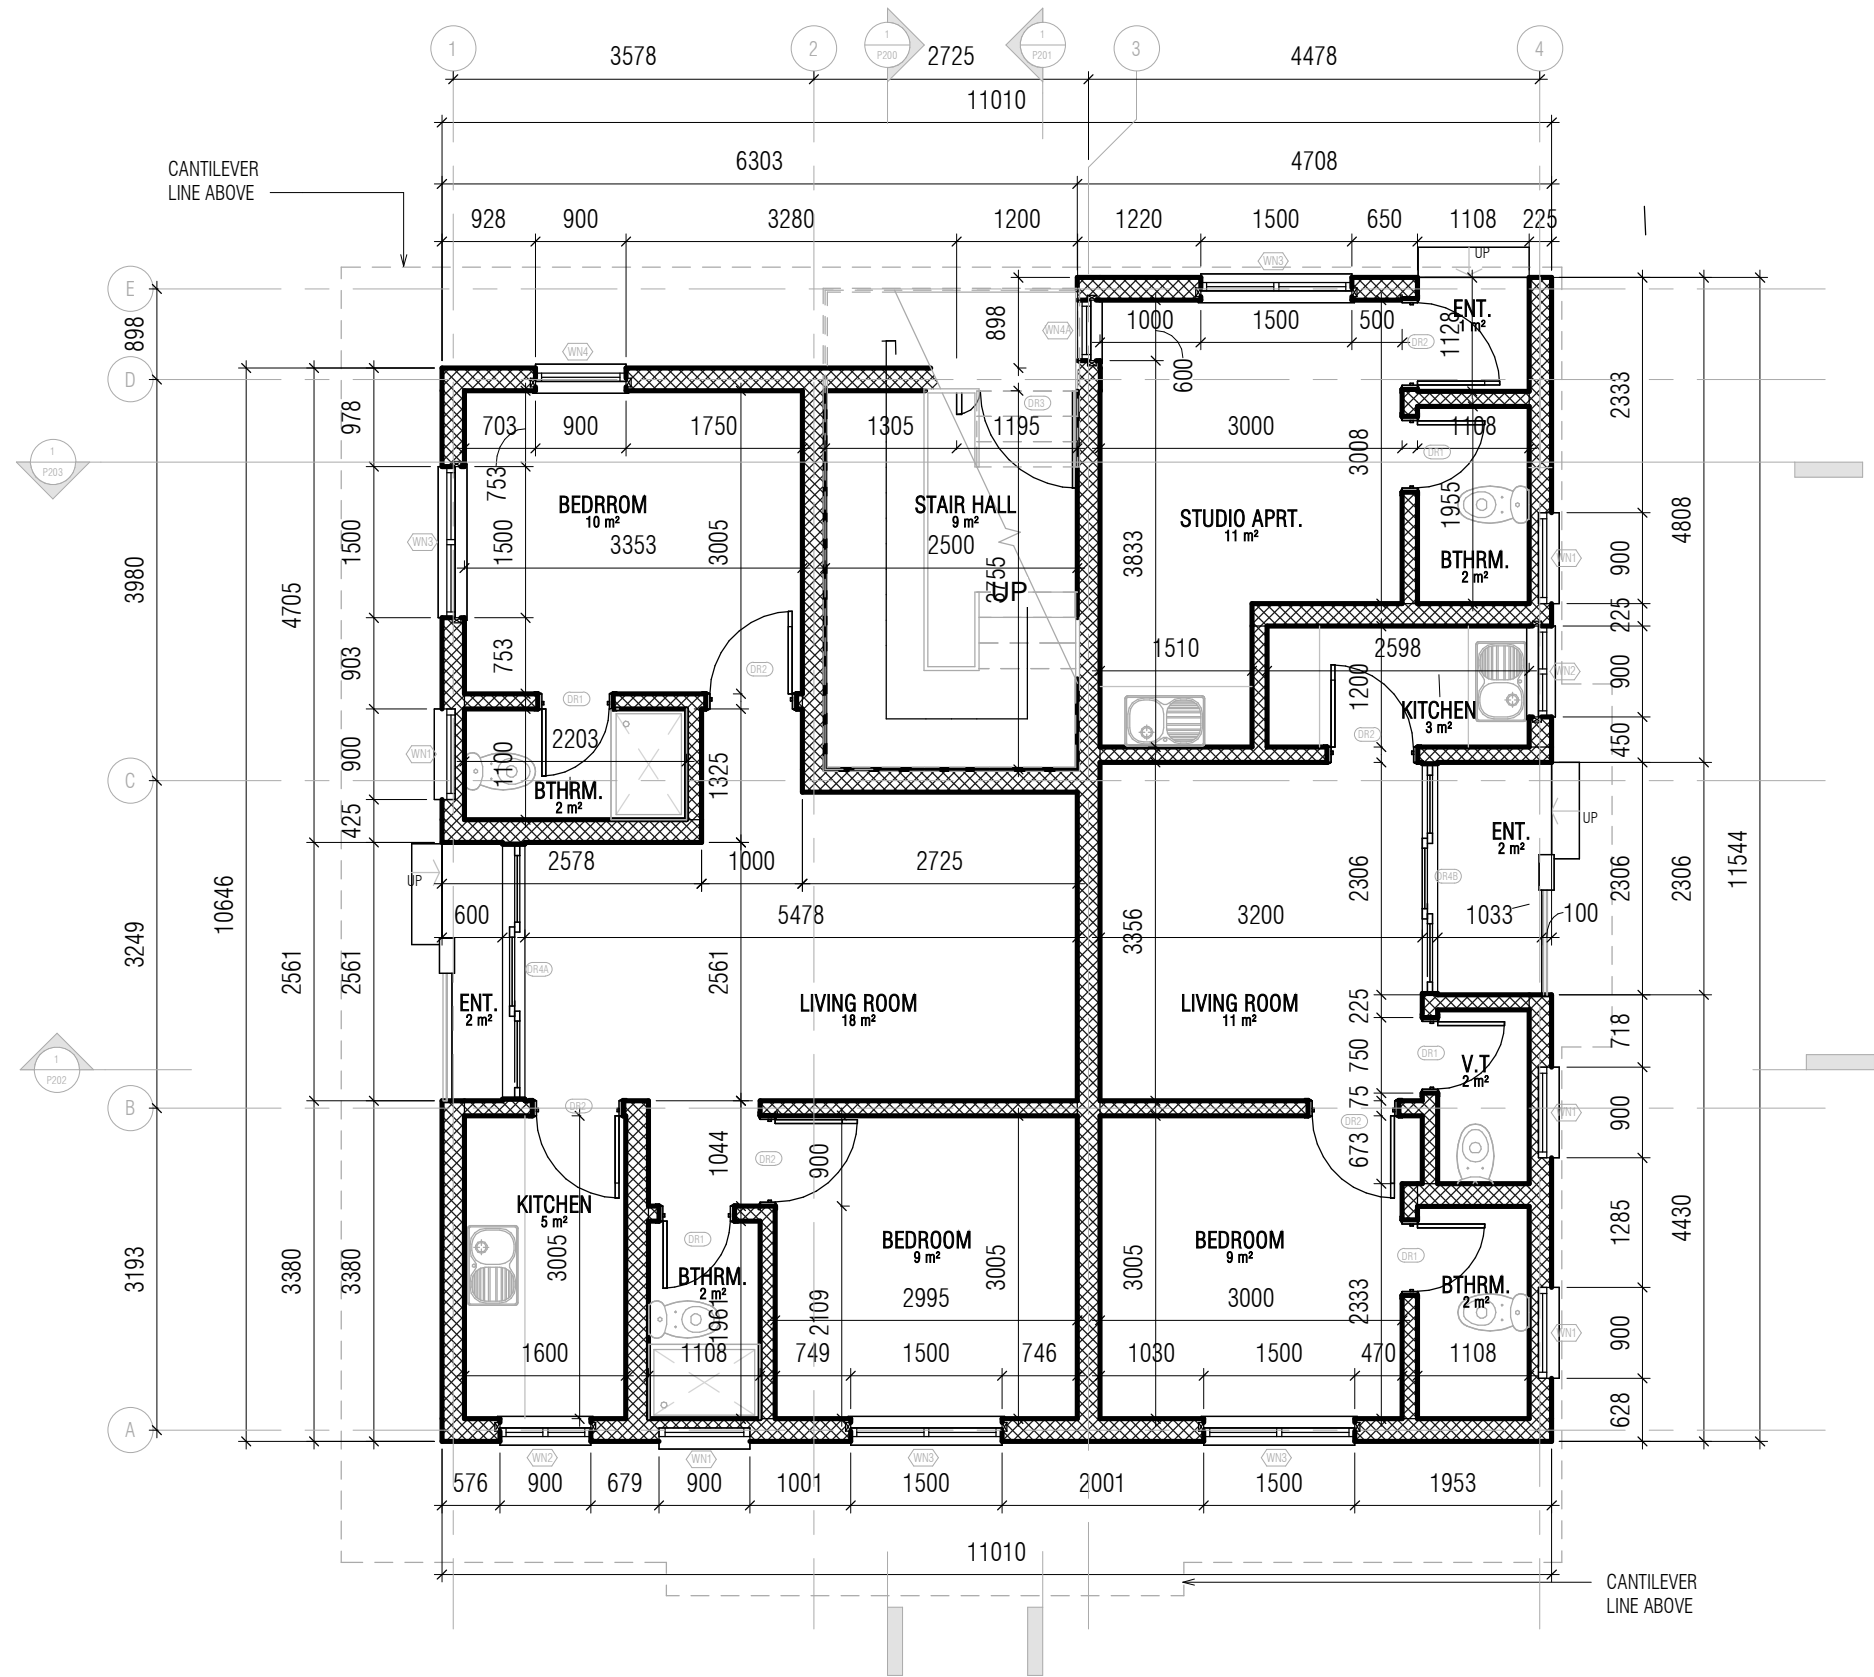


1 GROUND FLOOR PLAN
1 : 75



6A, OGUNLEYE STREET, AKOKA, LAGOS.

Project:	RESIDENTIAL DEVELOPMENT	Client:	DARALL HOMES LIMITED	Status:	Approval
Title:	GROUND FLOOR PLAN	Checked By:	A.H	Date/Rev:	2/18/2026 9:39:04 AM
Scale/Format:	1 : 75	Drawn By:	H.J	Sheet no:	P101

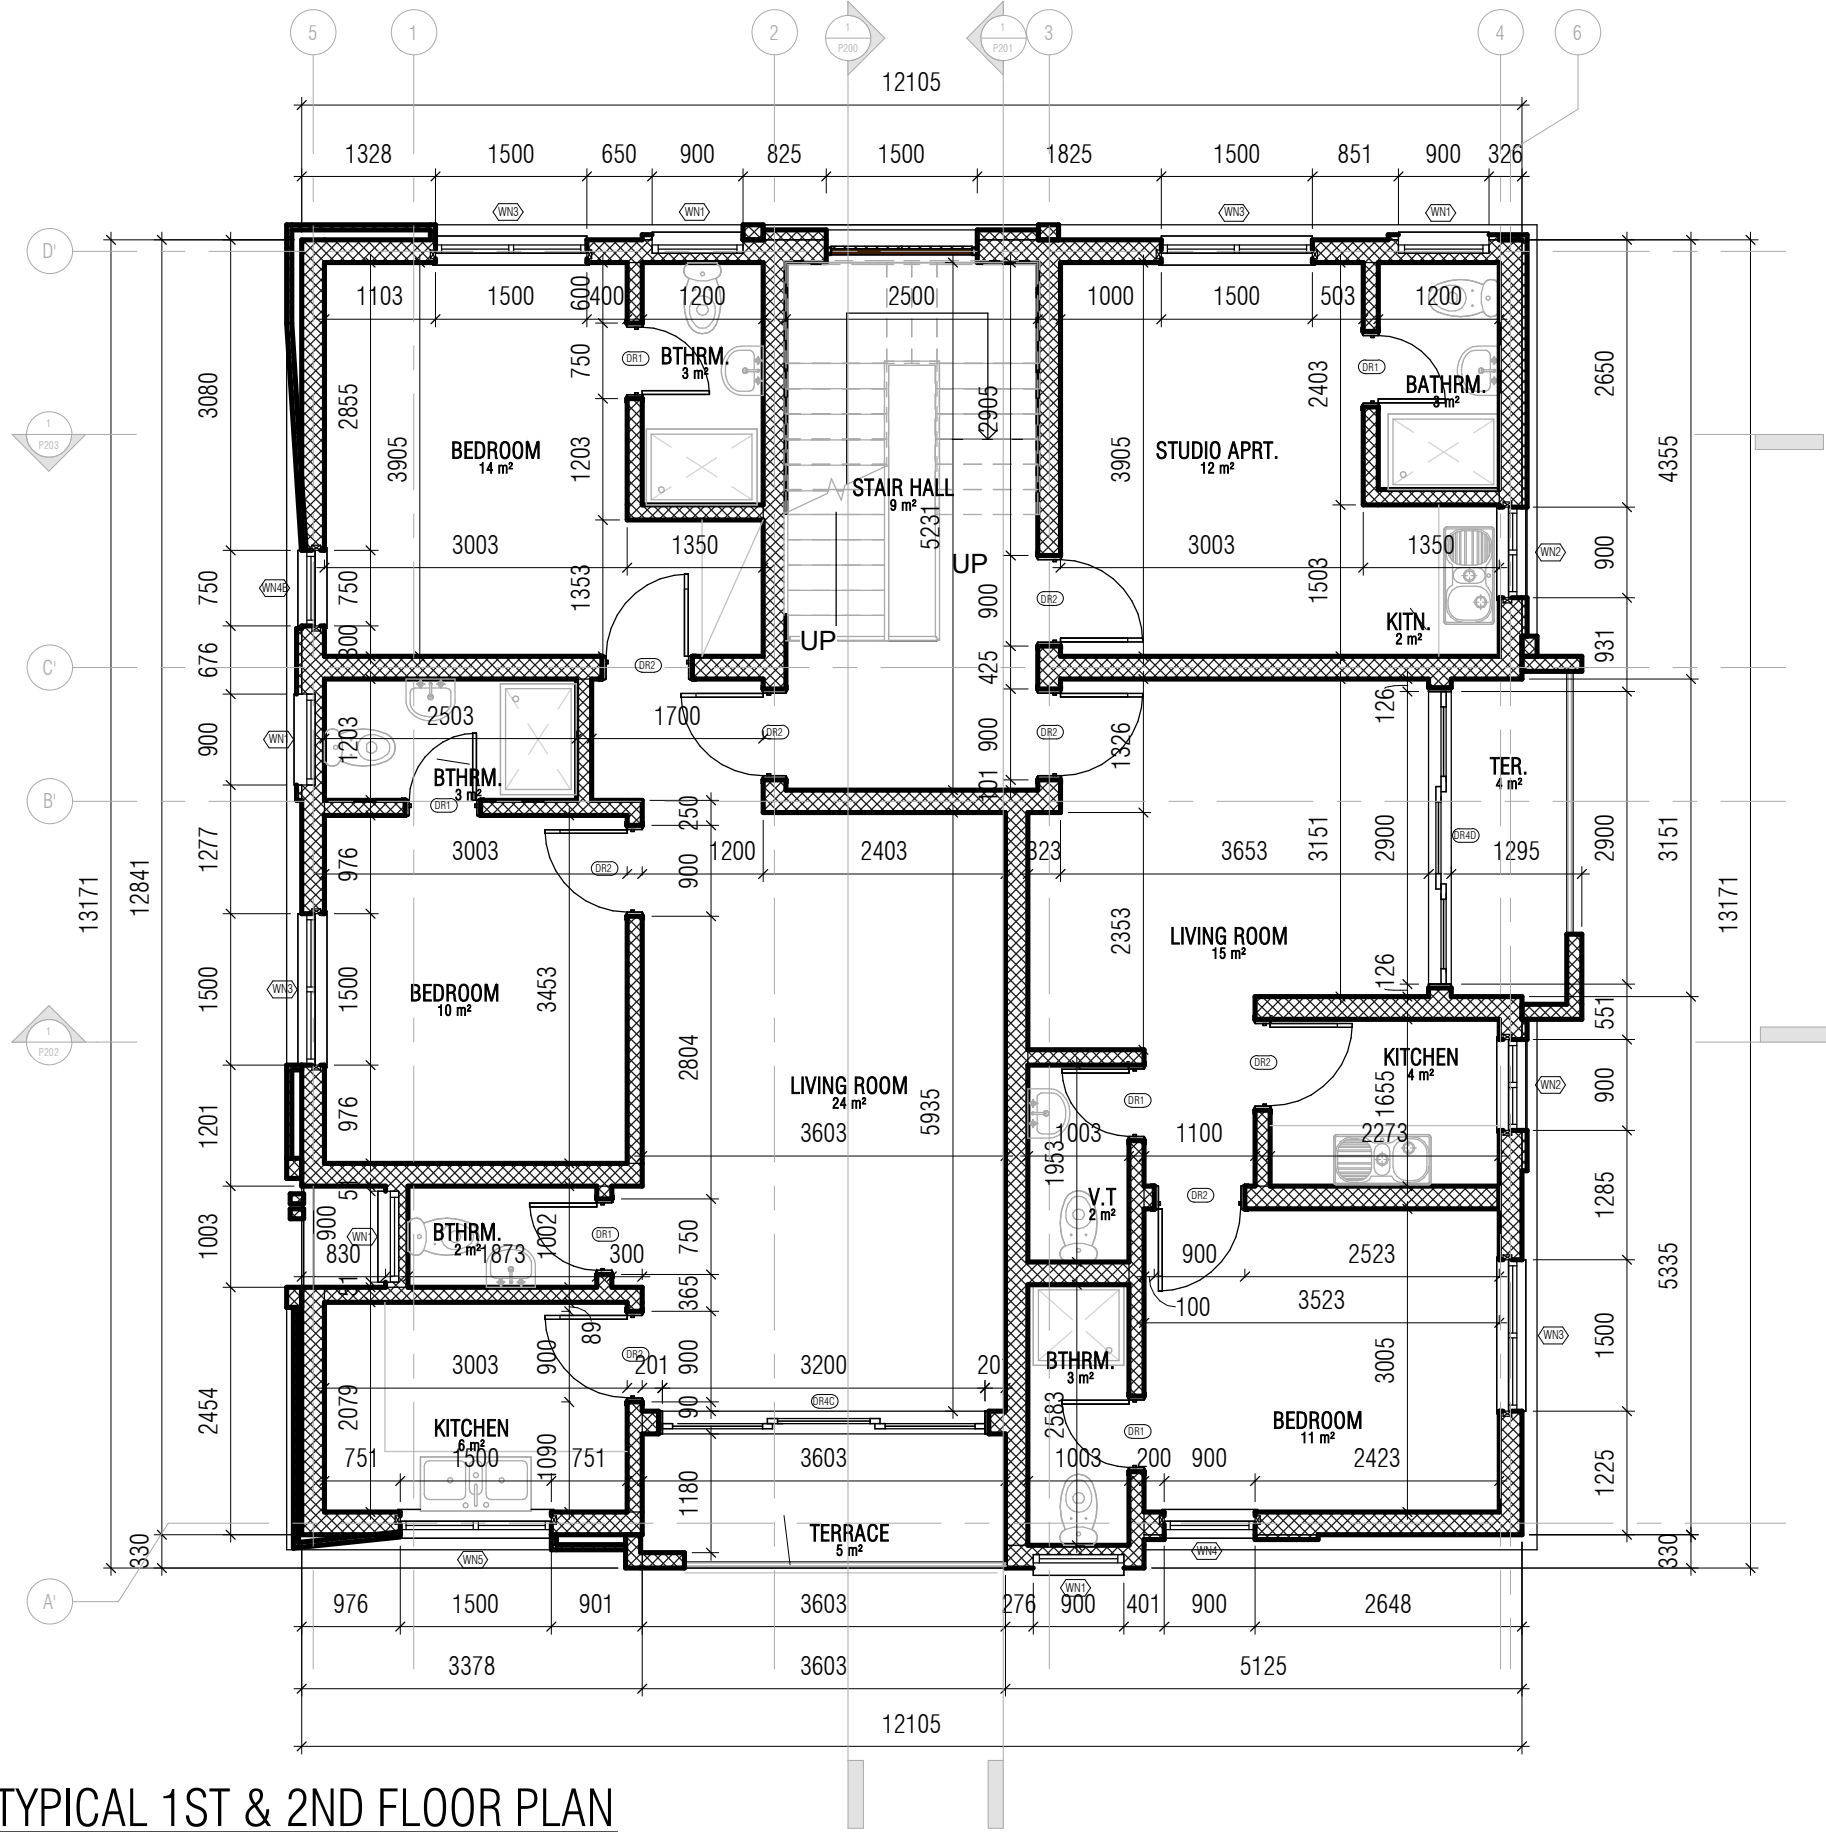


1 TYPICAL 1ST & 2ND FLOOR PLAN
1 : 75



6A, OGUNLEYE STREET, AKOKA, LAGOS.

Project: RESIDENTIAL DEVELOPMENT	Client: DARALL HOMES LIMITED	Status: Approval
Title: FIRST FLOOR PLAN	Checked By: A.H	Date/Rev: 2/18/2026 9:39:05 AM
Scale/Format: 1 : 75	Drawn By: H.J	Sheet no: P102

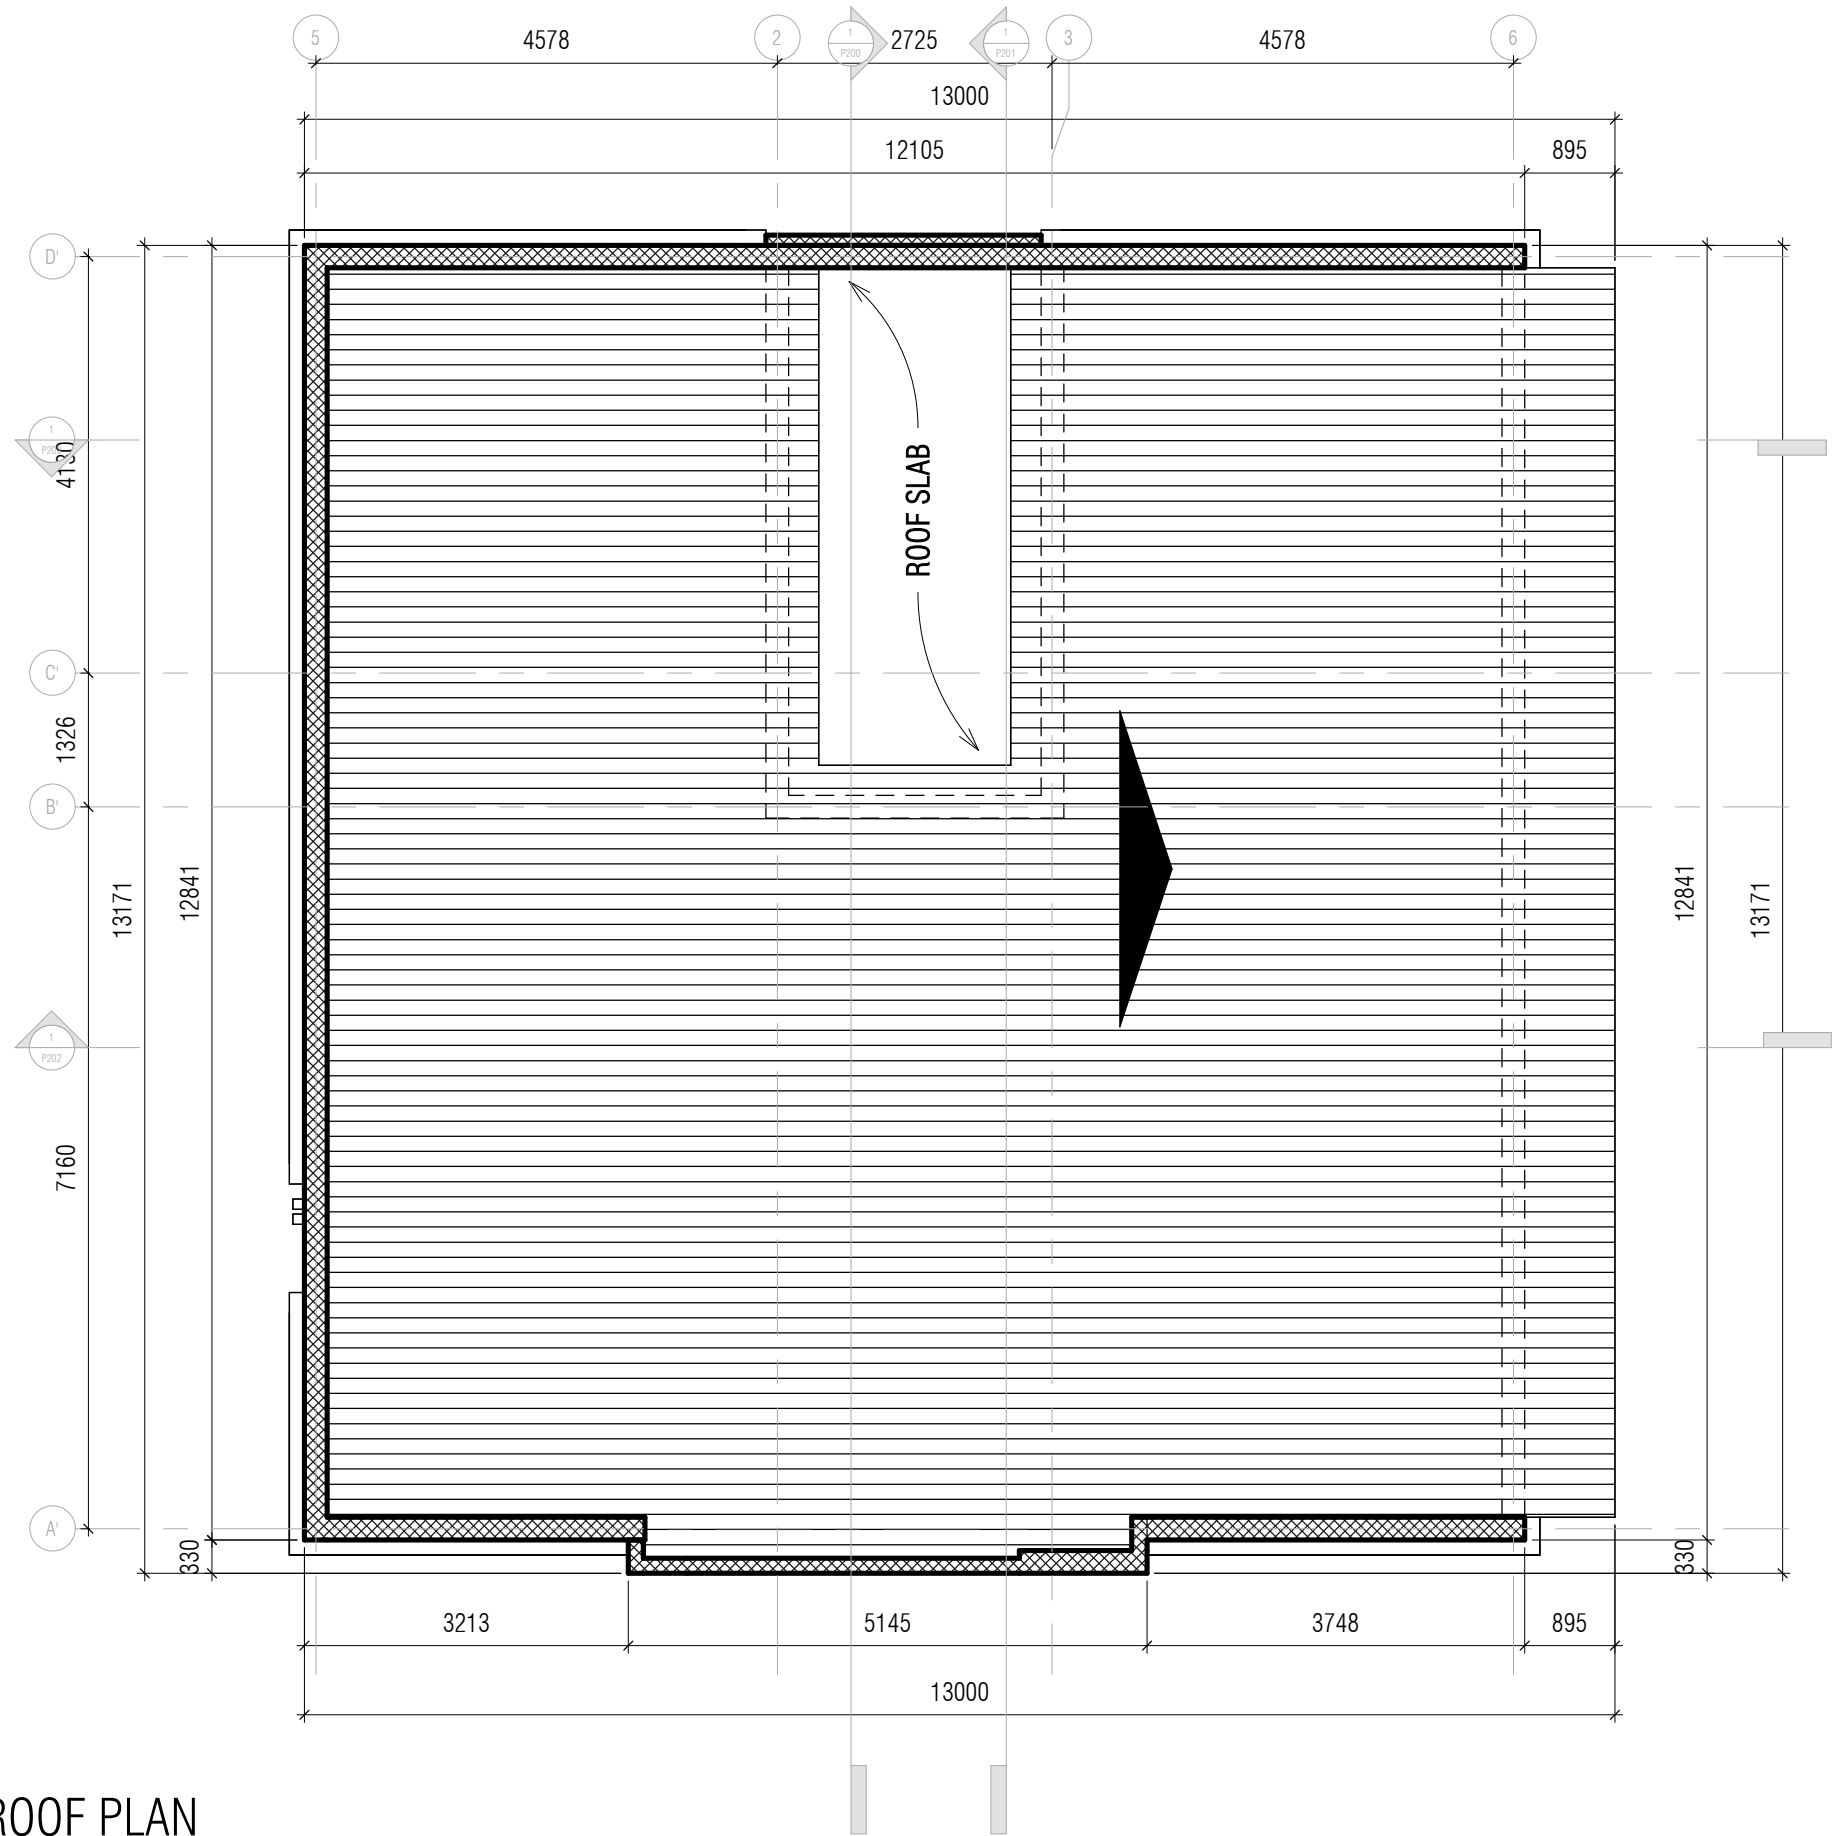


1 ROOF PLAN
1 : 75



6A, OGUNLEYE STREET, AKOKA, LAGOS.

Project: RESIDENTIAL DEVELOPMENT	Client: DARALL HOMES LIMITED	Status: Approval		
Title: ROOF PLAN	Checked By: A.H	Date/Rev: 2/18/2026 9:39:06 AM	Sheet no:	P103
Scale/Format: 1 : 75	Drawn By: H.J			

.7MM GAUGE, COLOUR COATED, LONGSPAN ALUMINIUM ROOFING SHEET ATTACHED TO 75X100MM WELL PLAINED HARDWOOD TIMBER PURLINS @ 900MM CENTERS ON 100X150MM, WELL PLAINED HARD WOOD TIMBER RAFTER @ 1200MM CENTERS. 150 mm RC ROOF SLAB TO BE TREATED WITH 2 LAYERS OF CONCRETE WATER PROOFING SOLUTION AND FINISH TO SLOPE TOWARD DRAIN POINT

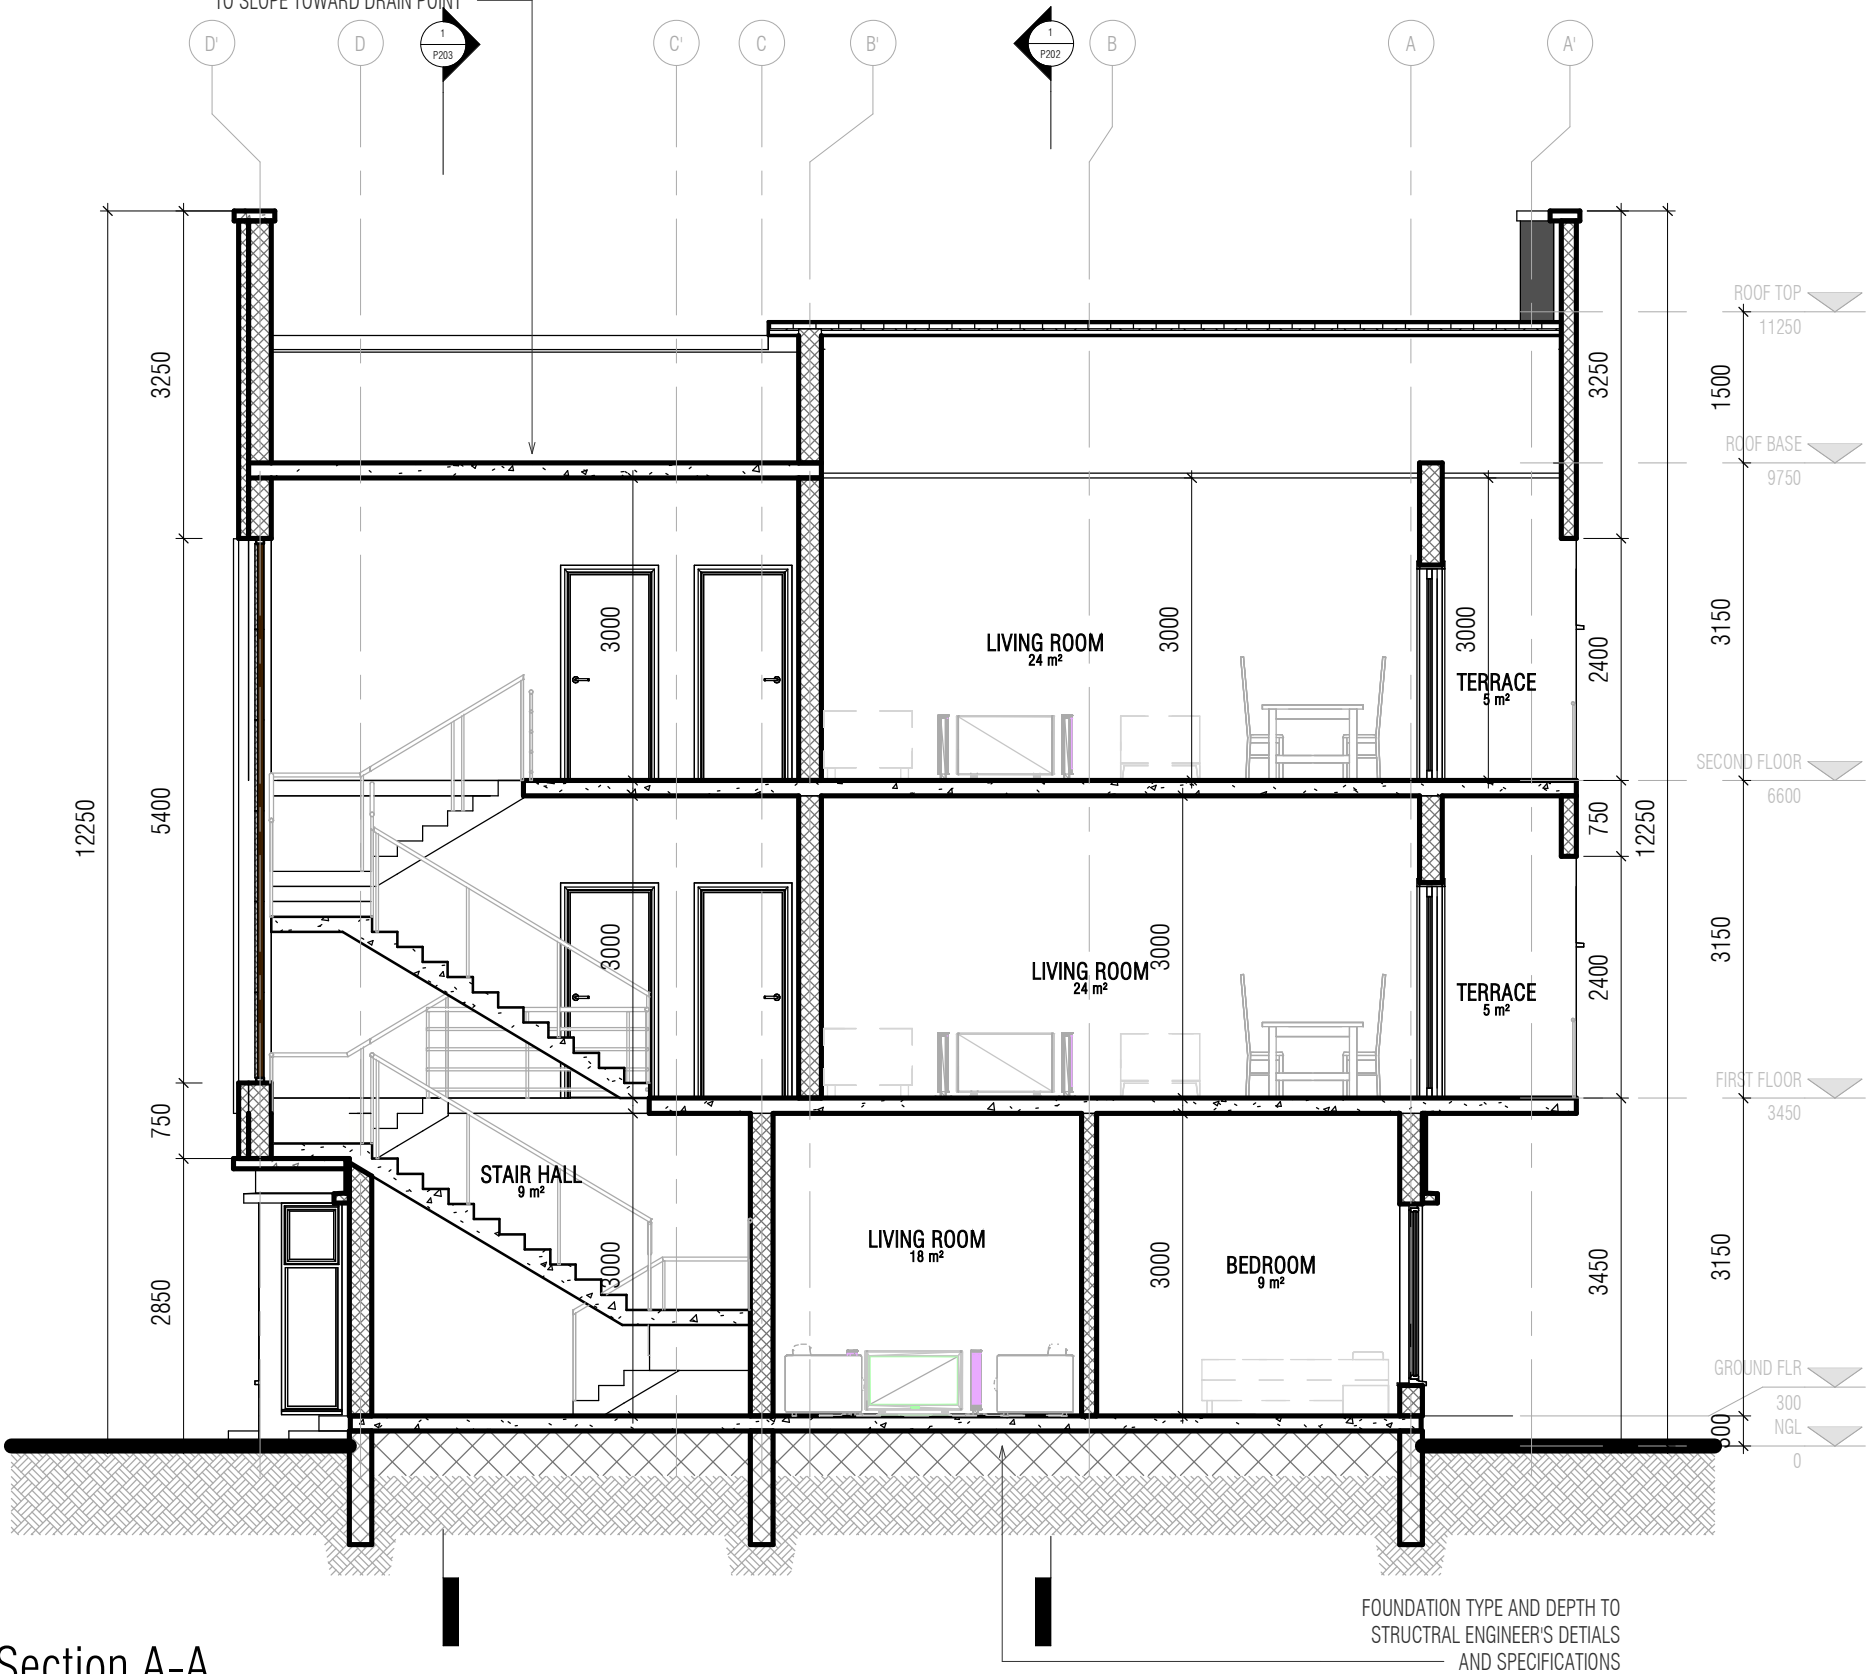


1 Section A-A
1 : 75



6A, OGUNLEYE STREET, AKOKA, LAGOS.

Project: RESIDENTIAL DEVELOPMENT	Client: DARALL HOMES LIMITED	Status: Approval
Title: SECTION A-A	Checked By: A.H	Date/Rev: 2/18/2026 9:39:07 AM
Scale/Format: 1 : 75	Drawn By: H.J	Sheet no: P200

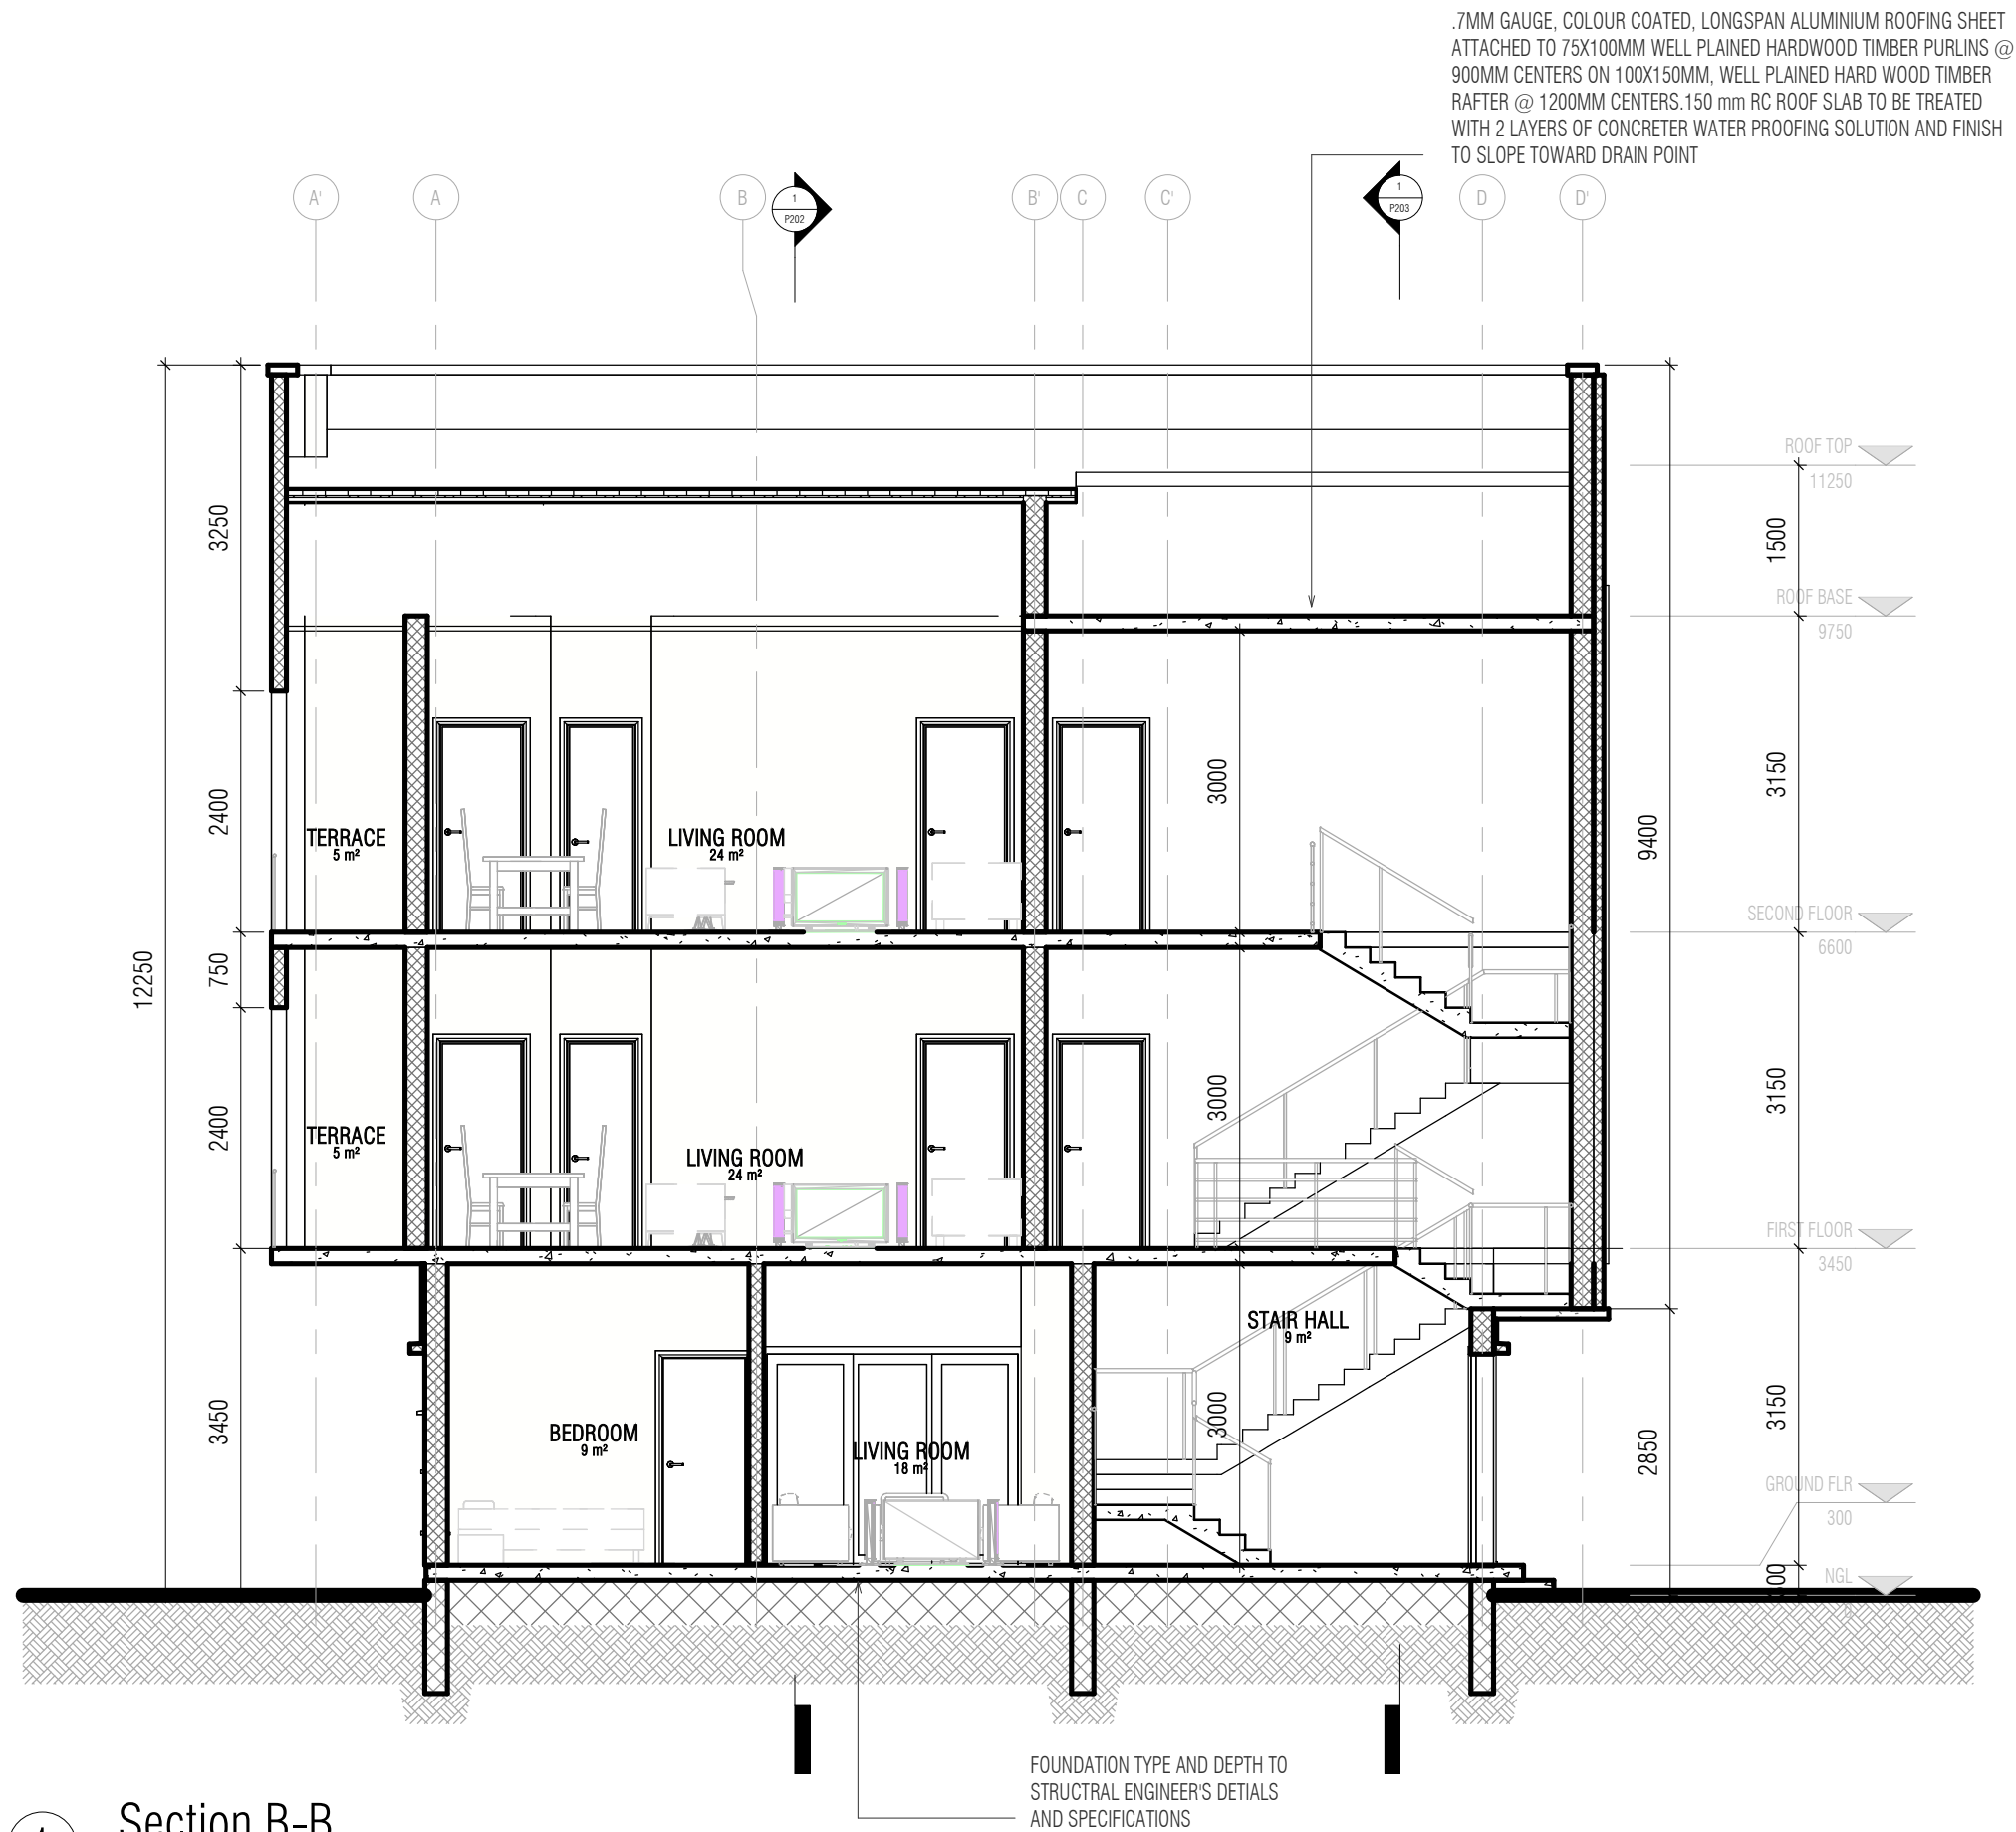

1 Section B-B
1 : 75



6A, OGUNLEYE STREET, AKOKA, LAGOS.

Project: RESIDENTIAL DEVELOPMENT

Client: DARALL HOMES LIMITED

Status: Approval

Title: SECTION B-B


Checked By: A.H

Date/Rev: 2/18/2026 9:39:10 AM

Sheet no: P201

Scale/Format: 1 : 75

Drawn By: H.J

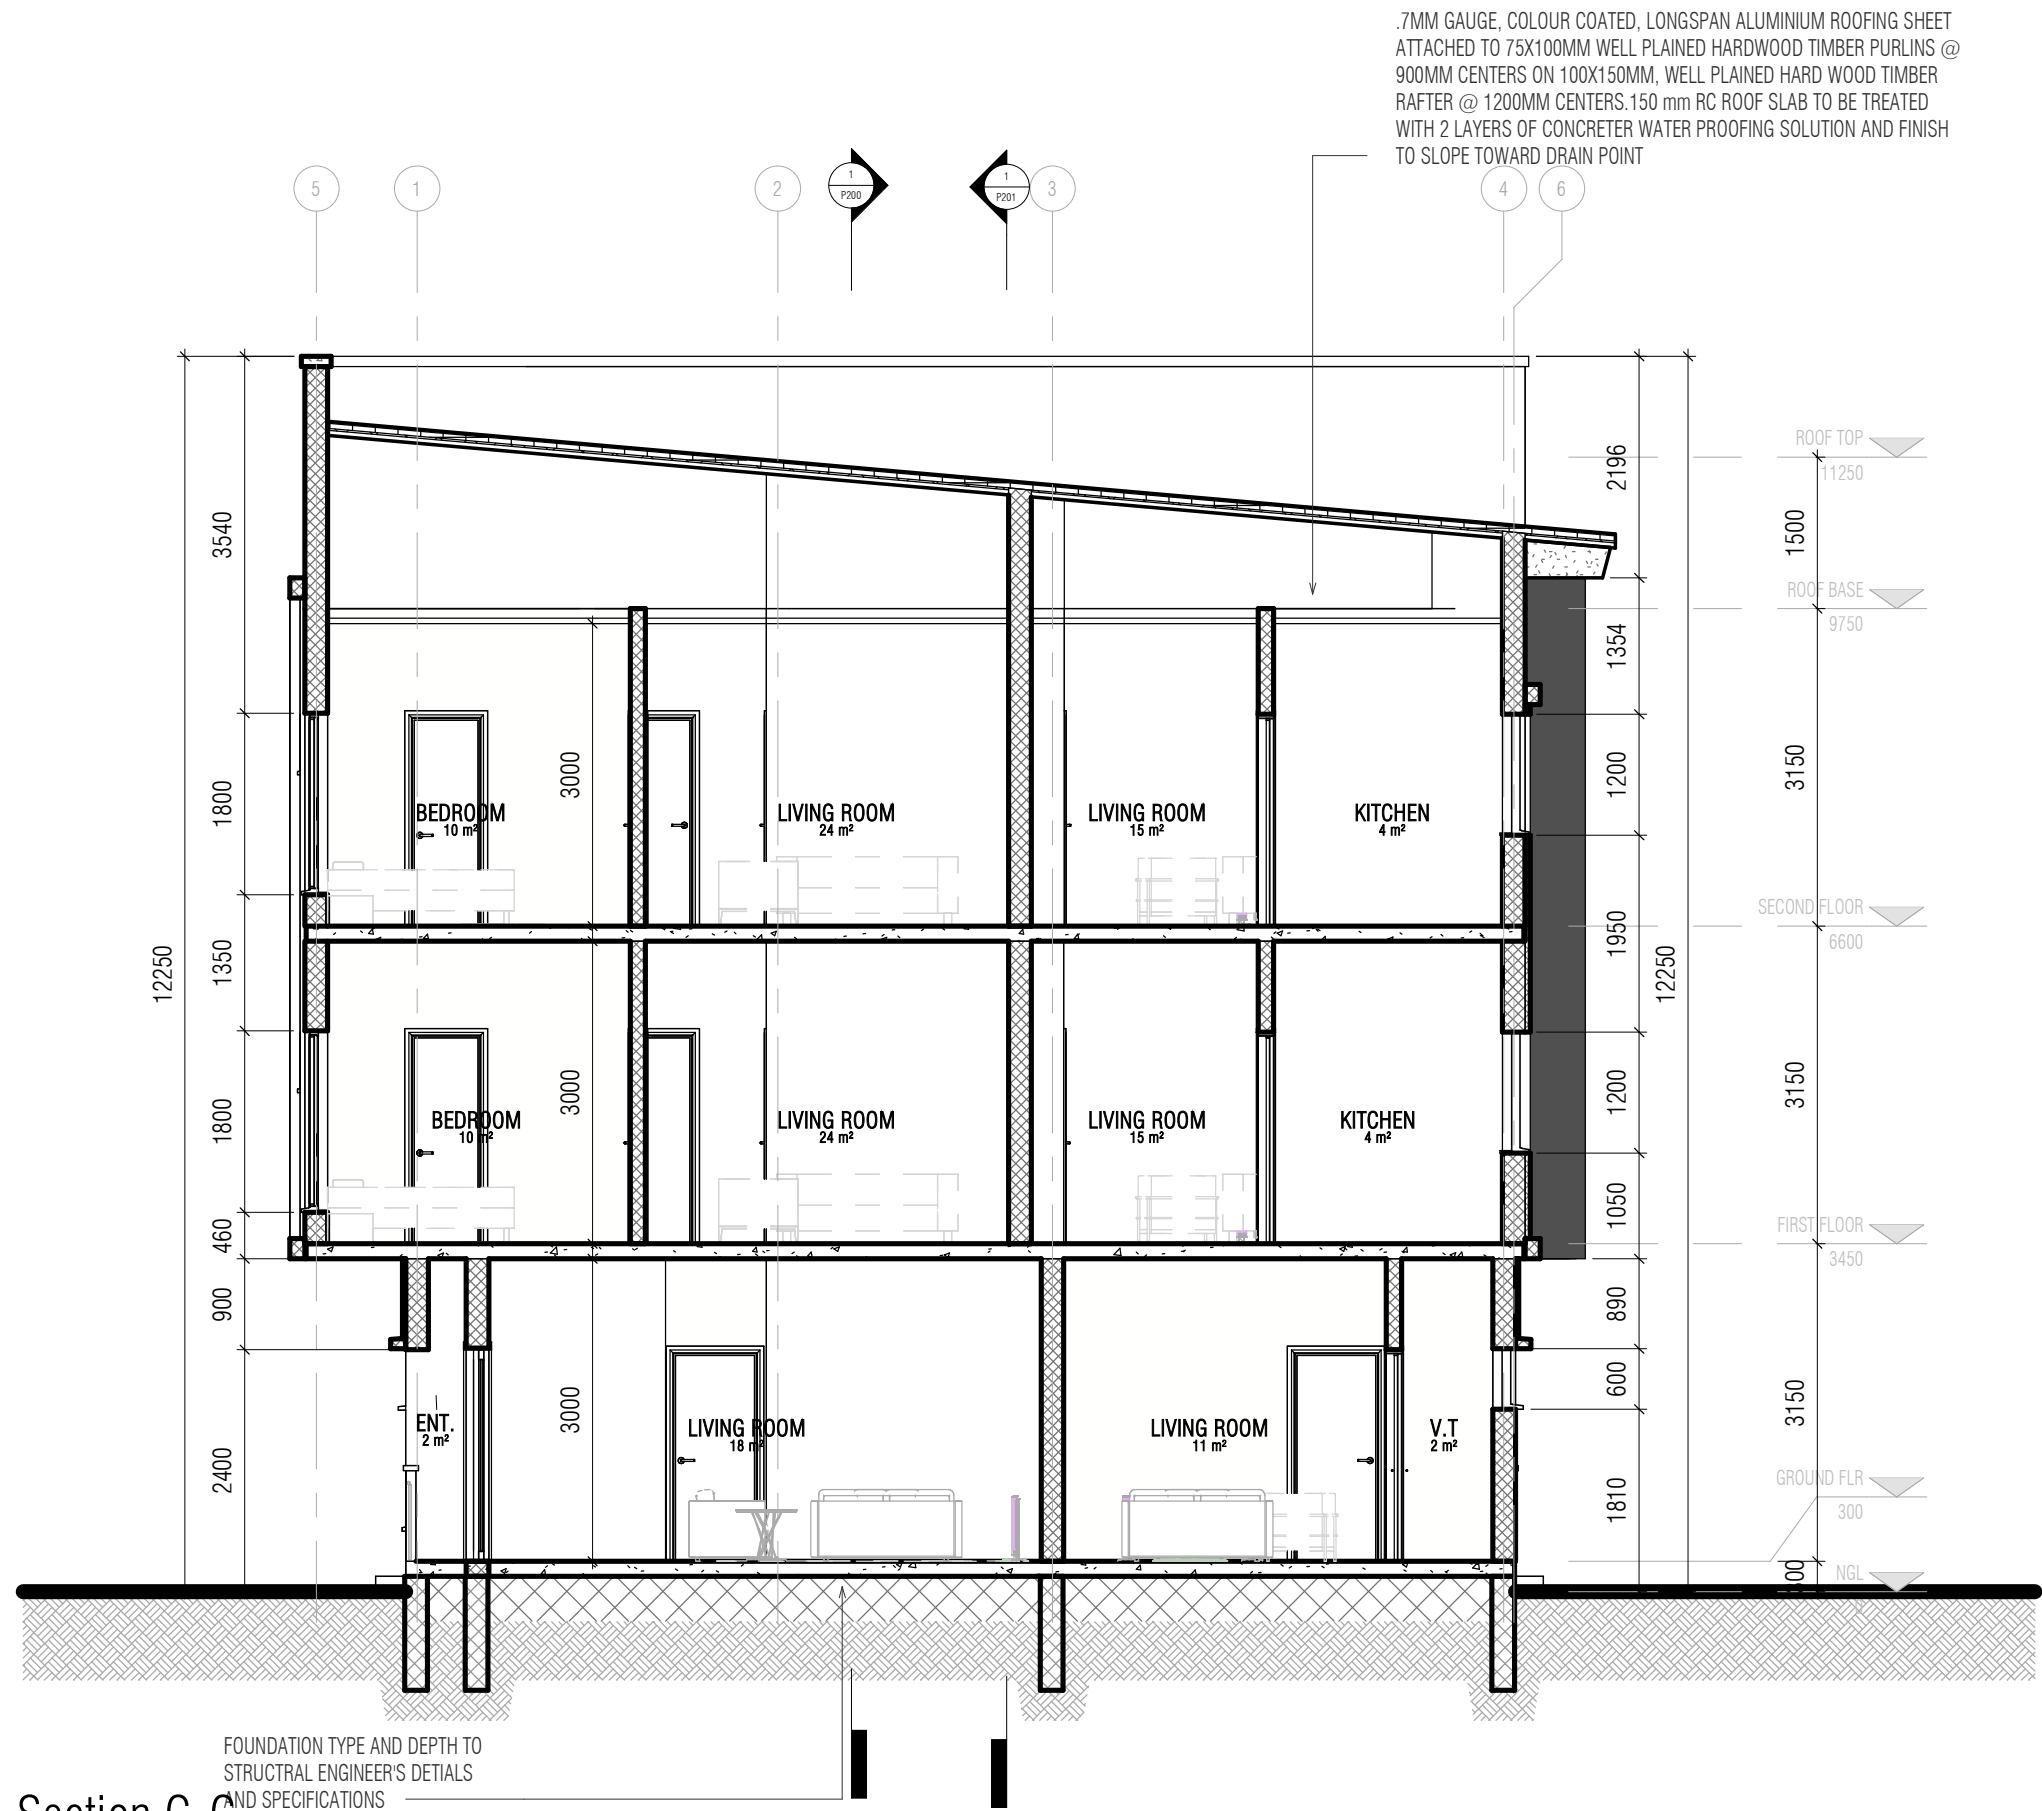


1 Section C-C
1 : 75



6A, OGUNLEYE STREET, AKOKA, LAGOS.

Project: RESIDENTIAL DEVELOPMENT	Client: DARALL HOMES LIMITED	Status: Approval
Title: SECTION C-C	Checked By: A.H	Date/Rev: 2/18/2026 9:39:14 AM
Scale/Format: 1 : 75	Drawn By: Author	Sheet no: P202

.7MM GAUGE, COLOUR COATED, LONGSPAN ALUMINIUM ROOFING SHEET
ATTACHED TO 75X100MM WELL PLAINED HARDWOOD TIMBER PURLINS @
900MM CENTERS ON 100X150MM, WELL PLAINED HARD WOOD TIMBER
RAFTER @ 1200MM CENTERS.150 mm RC ROOF SLAB TO BE TREATED
WITH 2 LAYERS OF CONCRETE WATER PROOFING SOLUTION AND FINISH
TO SLOPE TOWARD DRAIN POINT

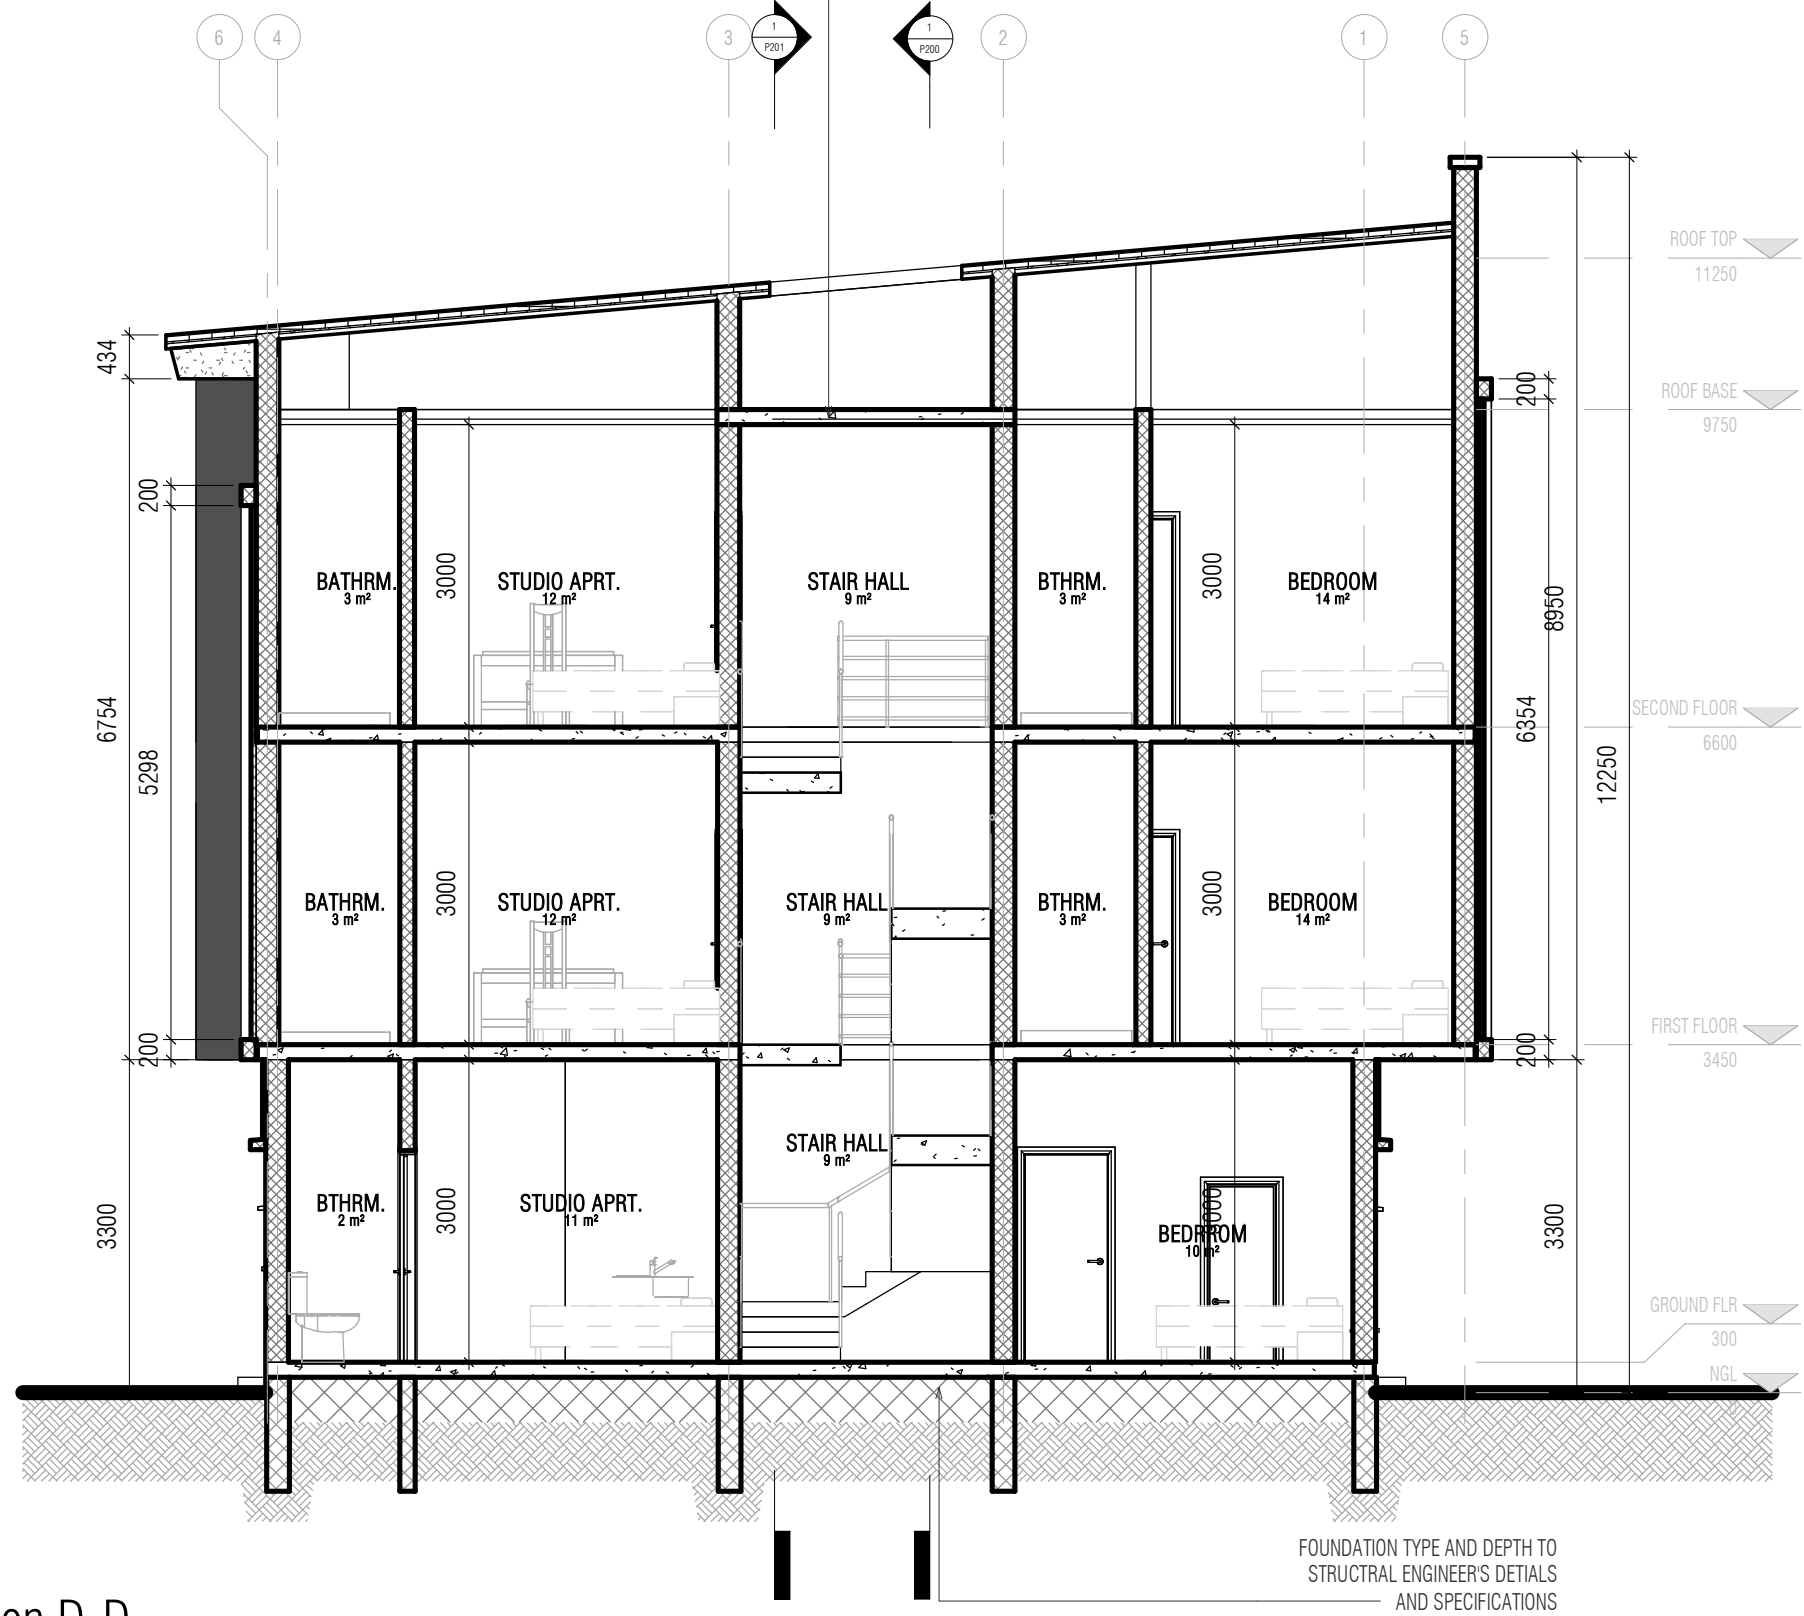

1 Section D-D
1 : 75



6A, OGUNLEYE STREET, AKOKA, LAGOS.

Project: RESIDENTIAL DEVELOPMENT

Client: DARALL HOMES LIMITED

Status: Approval

Title: SECTION D-D


Checked By: A.H

Date/Rev: 2/18/2026 9:39:17 AM

Sheet no: P203

Scale/Format: 1 : 75

Drawn By: H.J

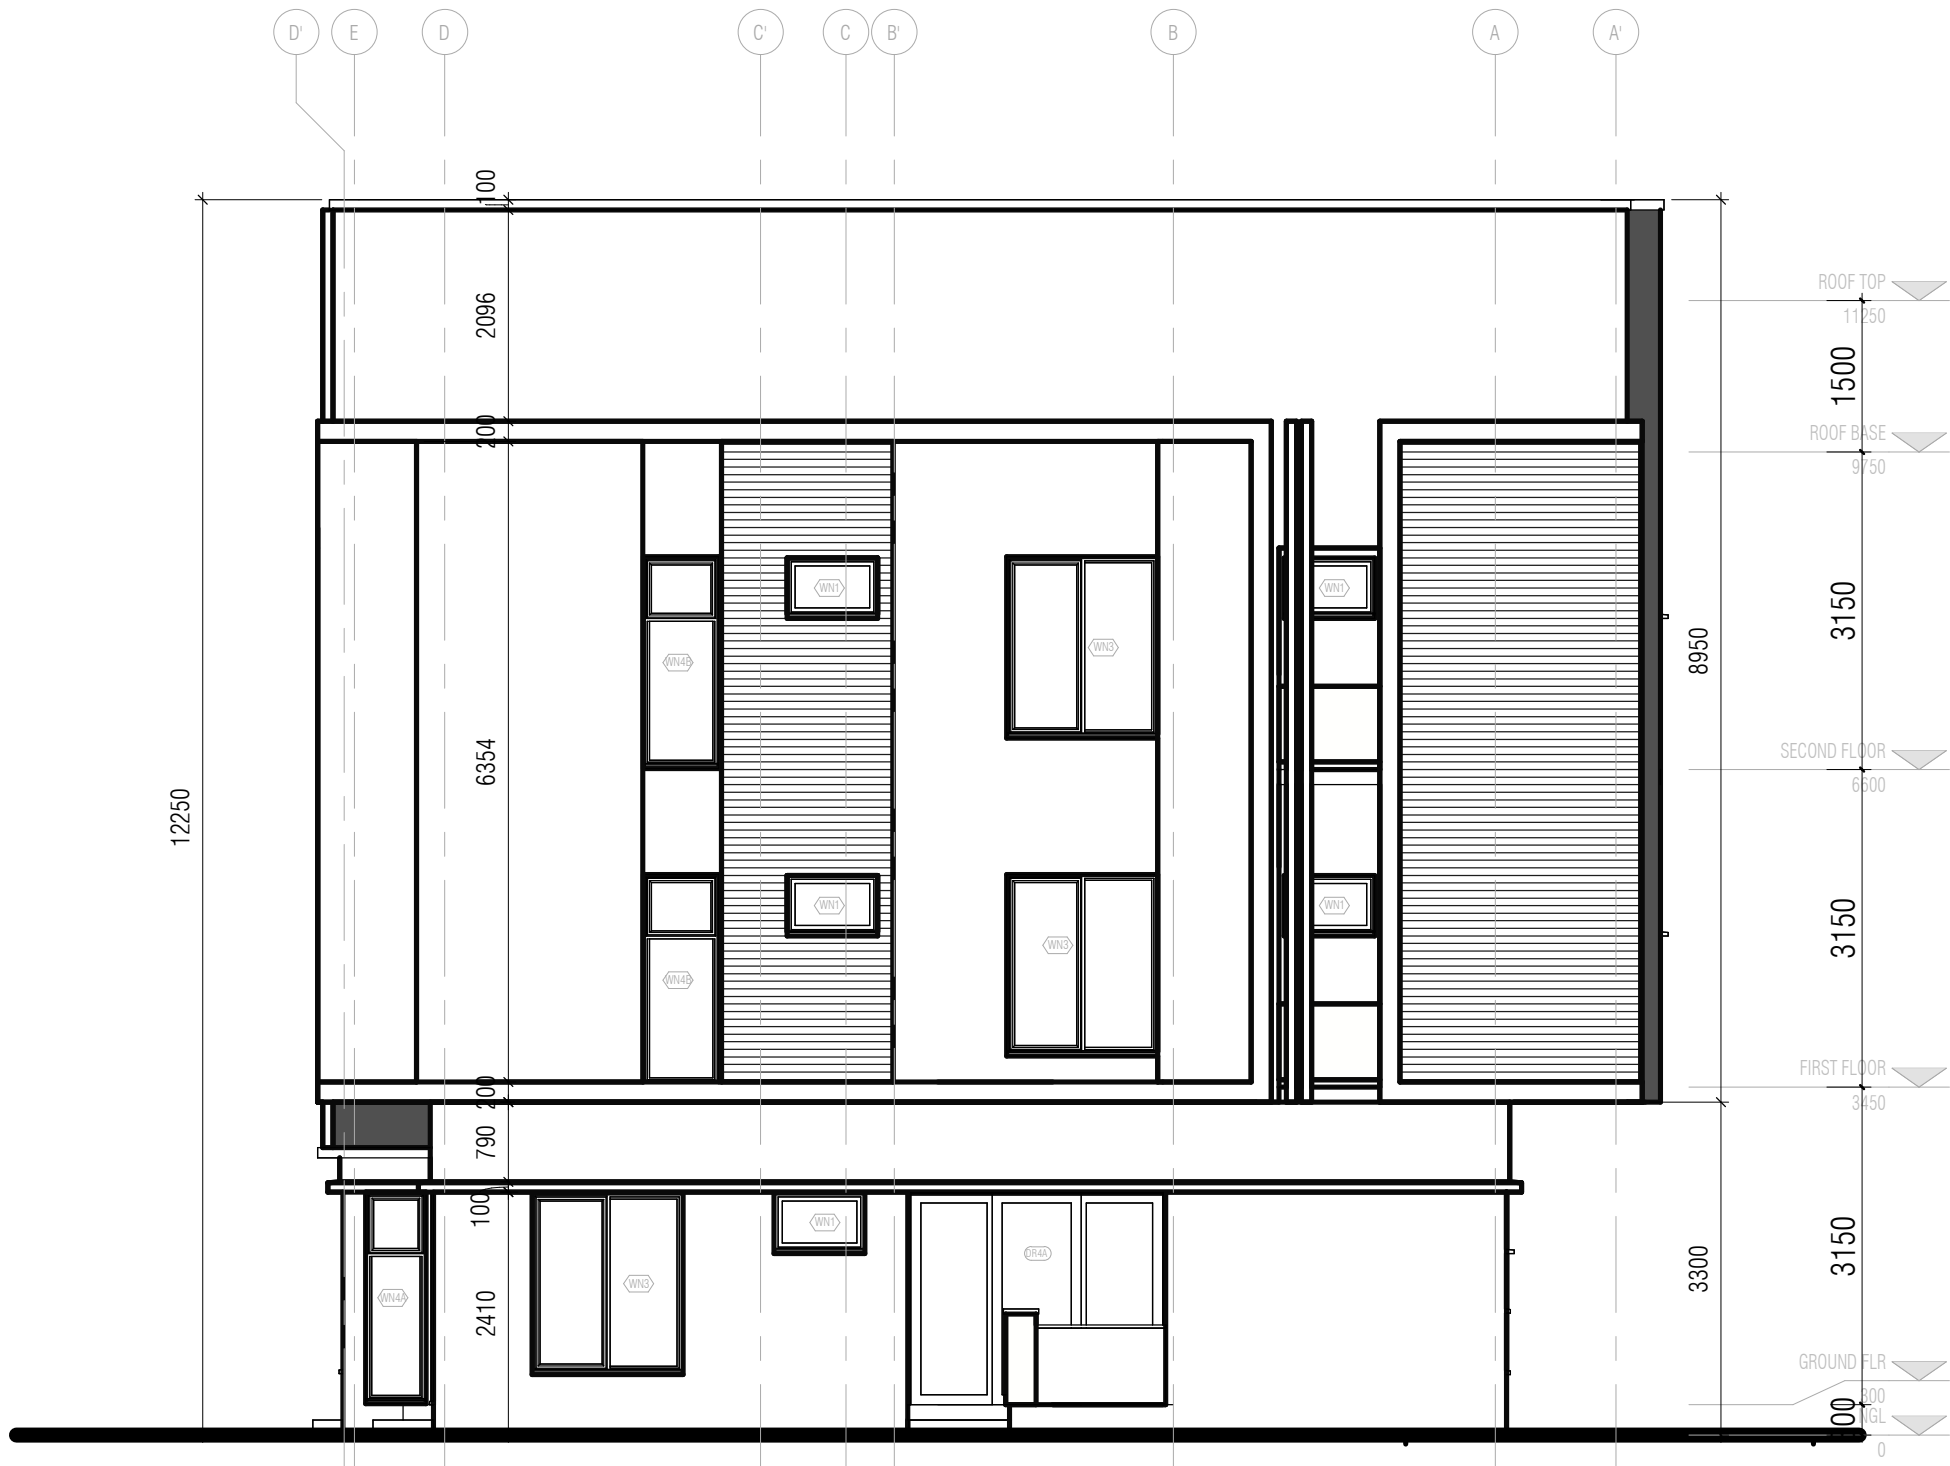


1 Front Elevation
1 : 75



6A, OGUNLEYE STREET, AKOKA, LAGOS.

Project:	RESIDENTIAL DEVELOPMENT	Client:	DARALL HOMES LIMITED	Status:	Approval
Title:	FRONT ELEVATION	Checked By:	A.H	Date/Rev:	2/18/2026 9:39:18 AM
Scale/Format:	1 : 75	Drawn By:	H.J	Sheet no:	P220

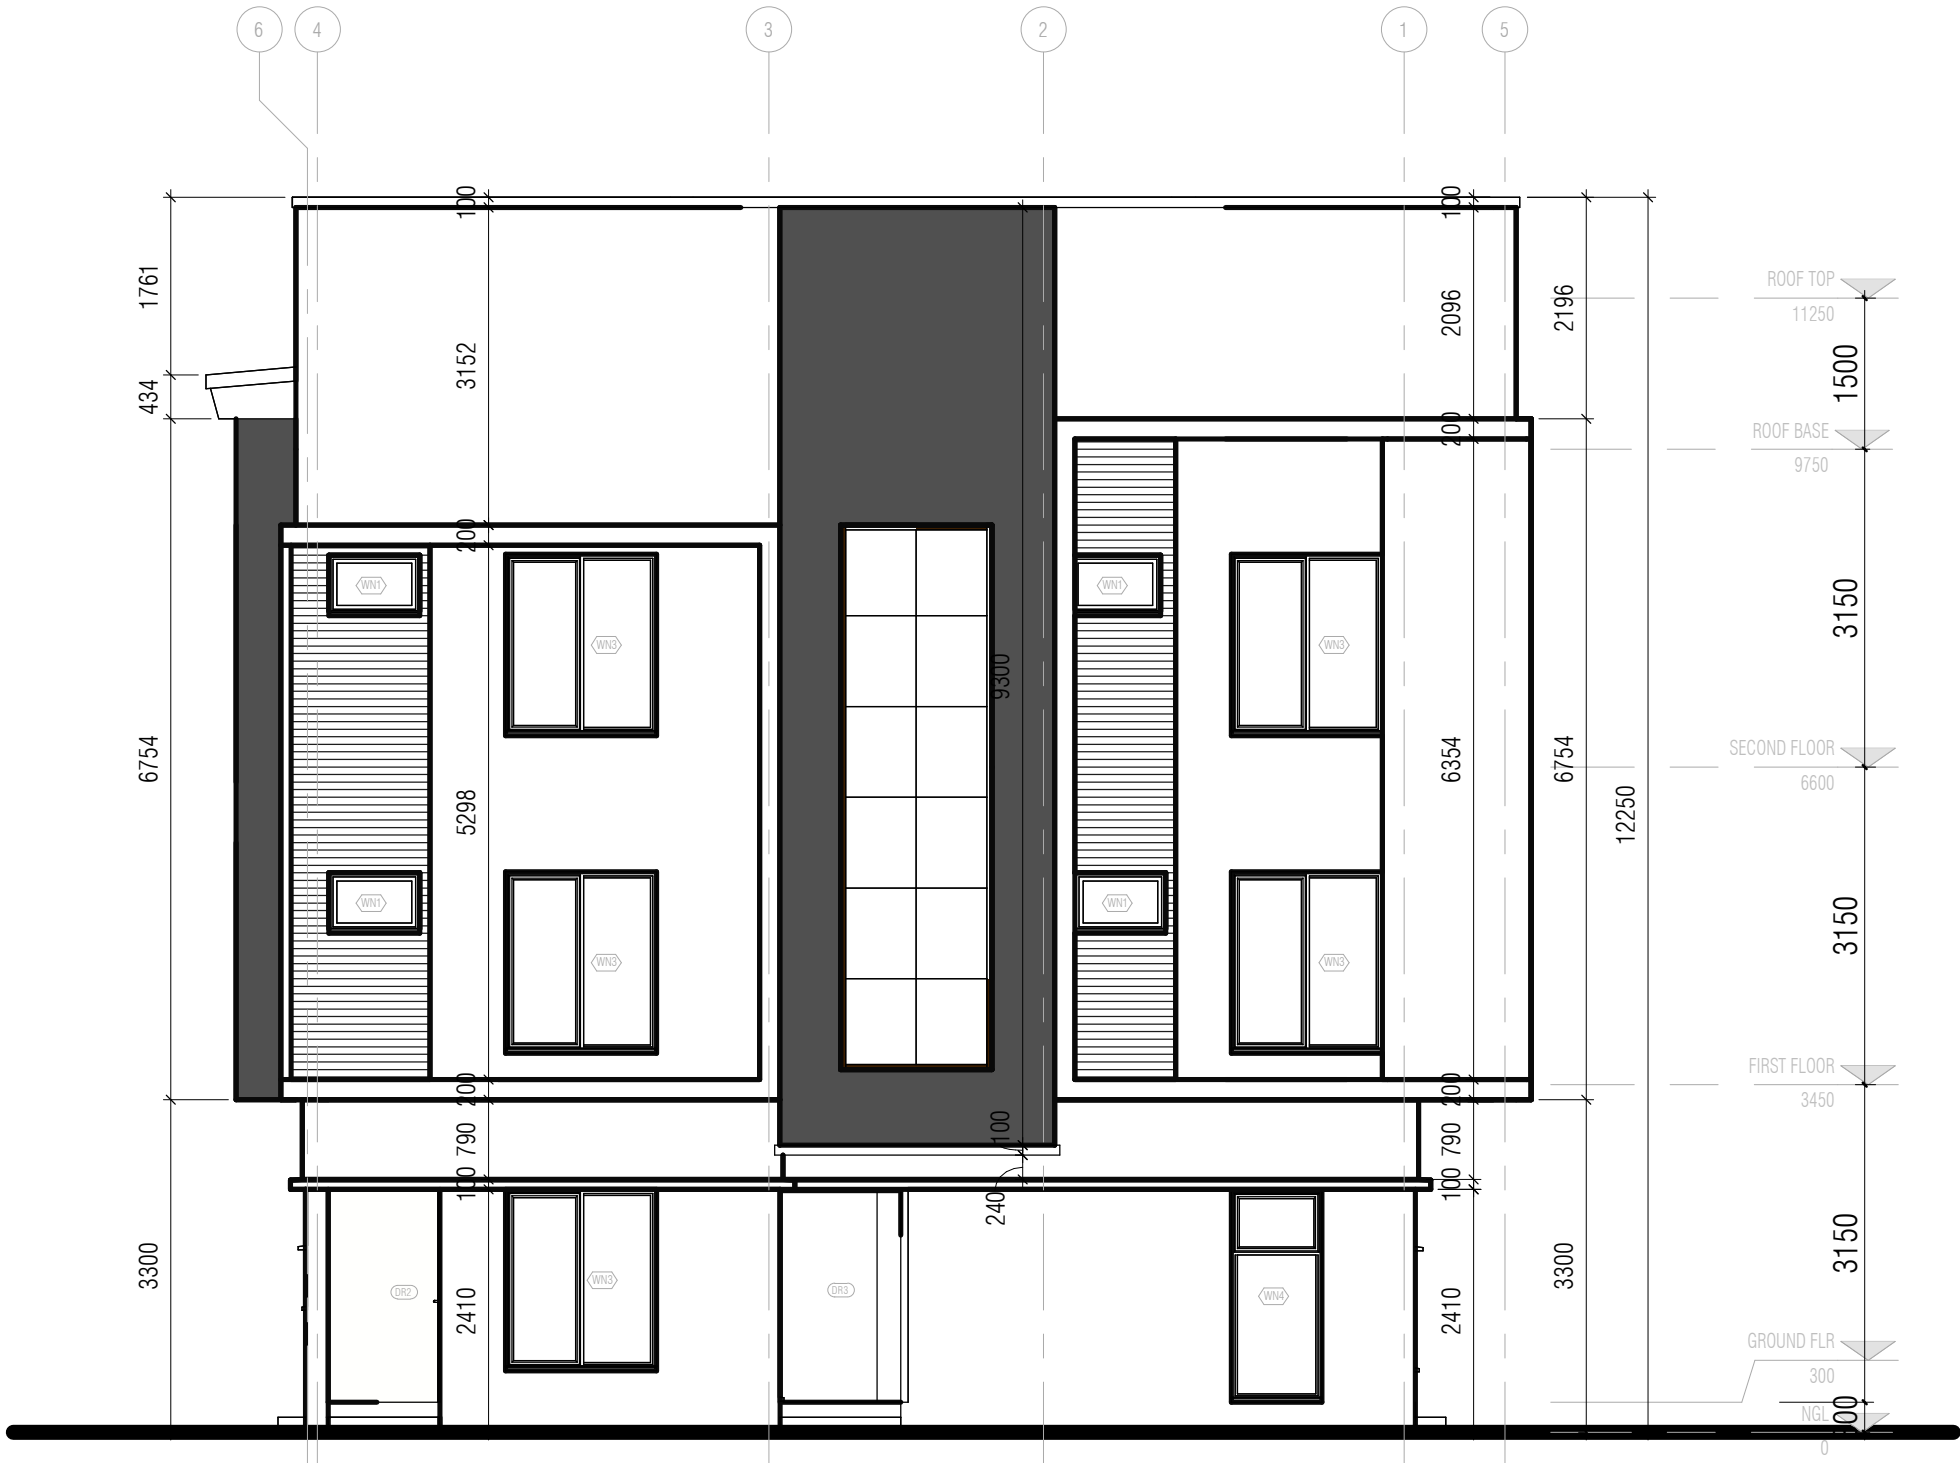

1 Left Elevation
1 : 75



6A, OGUNLEYE STREET, AKOKA, LAGOS.

Project: RESIDENTIAL DEVELOPMENT	Client: DARALL HOMES LIMITED	Status: Approval
Title: LEFT ELEVATION	Checked By: A.H	Date/Rev: 2/18/2026 9:39:19 AM
Scale/Format: 1 : 75	Drawn By: H.J	Sheet no: P221




1 Back Elevation
1 : 75



6A, OGUNLEYE STREET, AKOKA, LAGOS.

Project: RESIDENTIAL DEVELOPMENT	Client: DARALL HOMES LIMITED	Status: Approval
Title: BACK ELEVATION	Checked By: A.H	Date/Rev: 2/18/2026 9:39:20 AM
Scale/Format: 1 : 75	Drawn By: H.J	Sheet no: P222

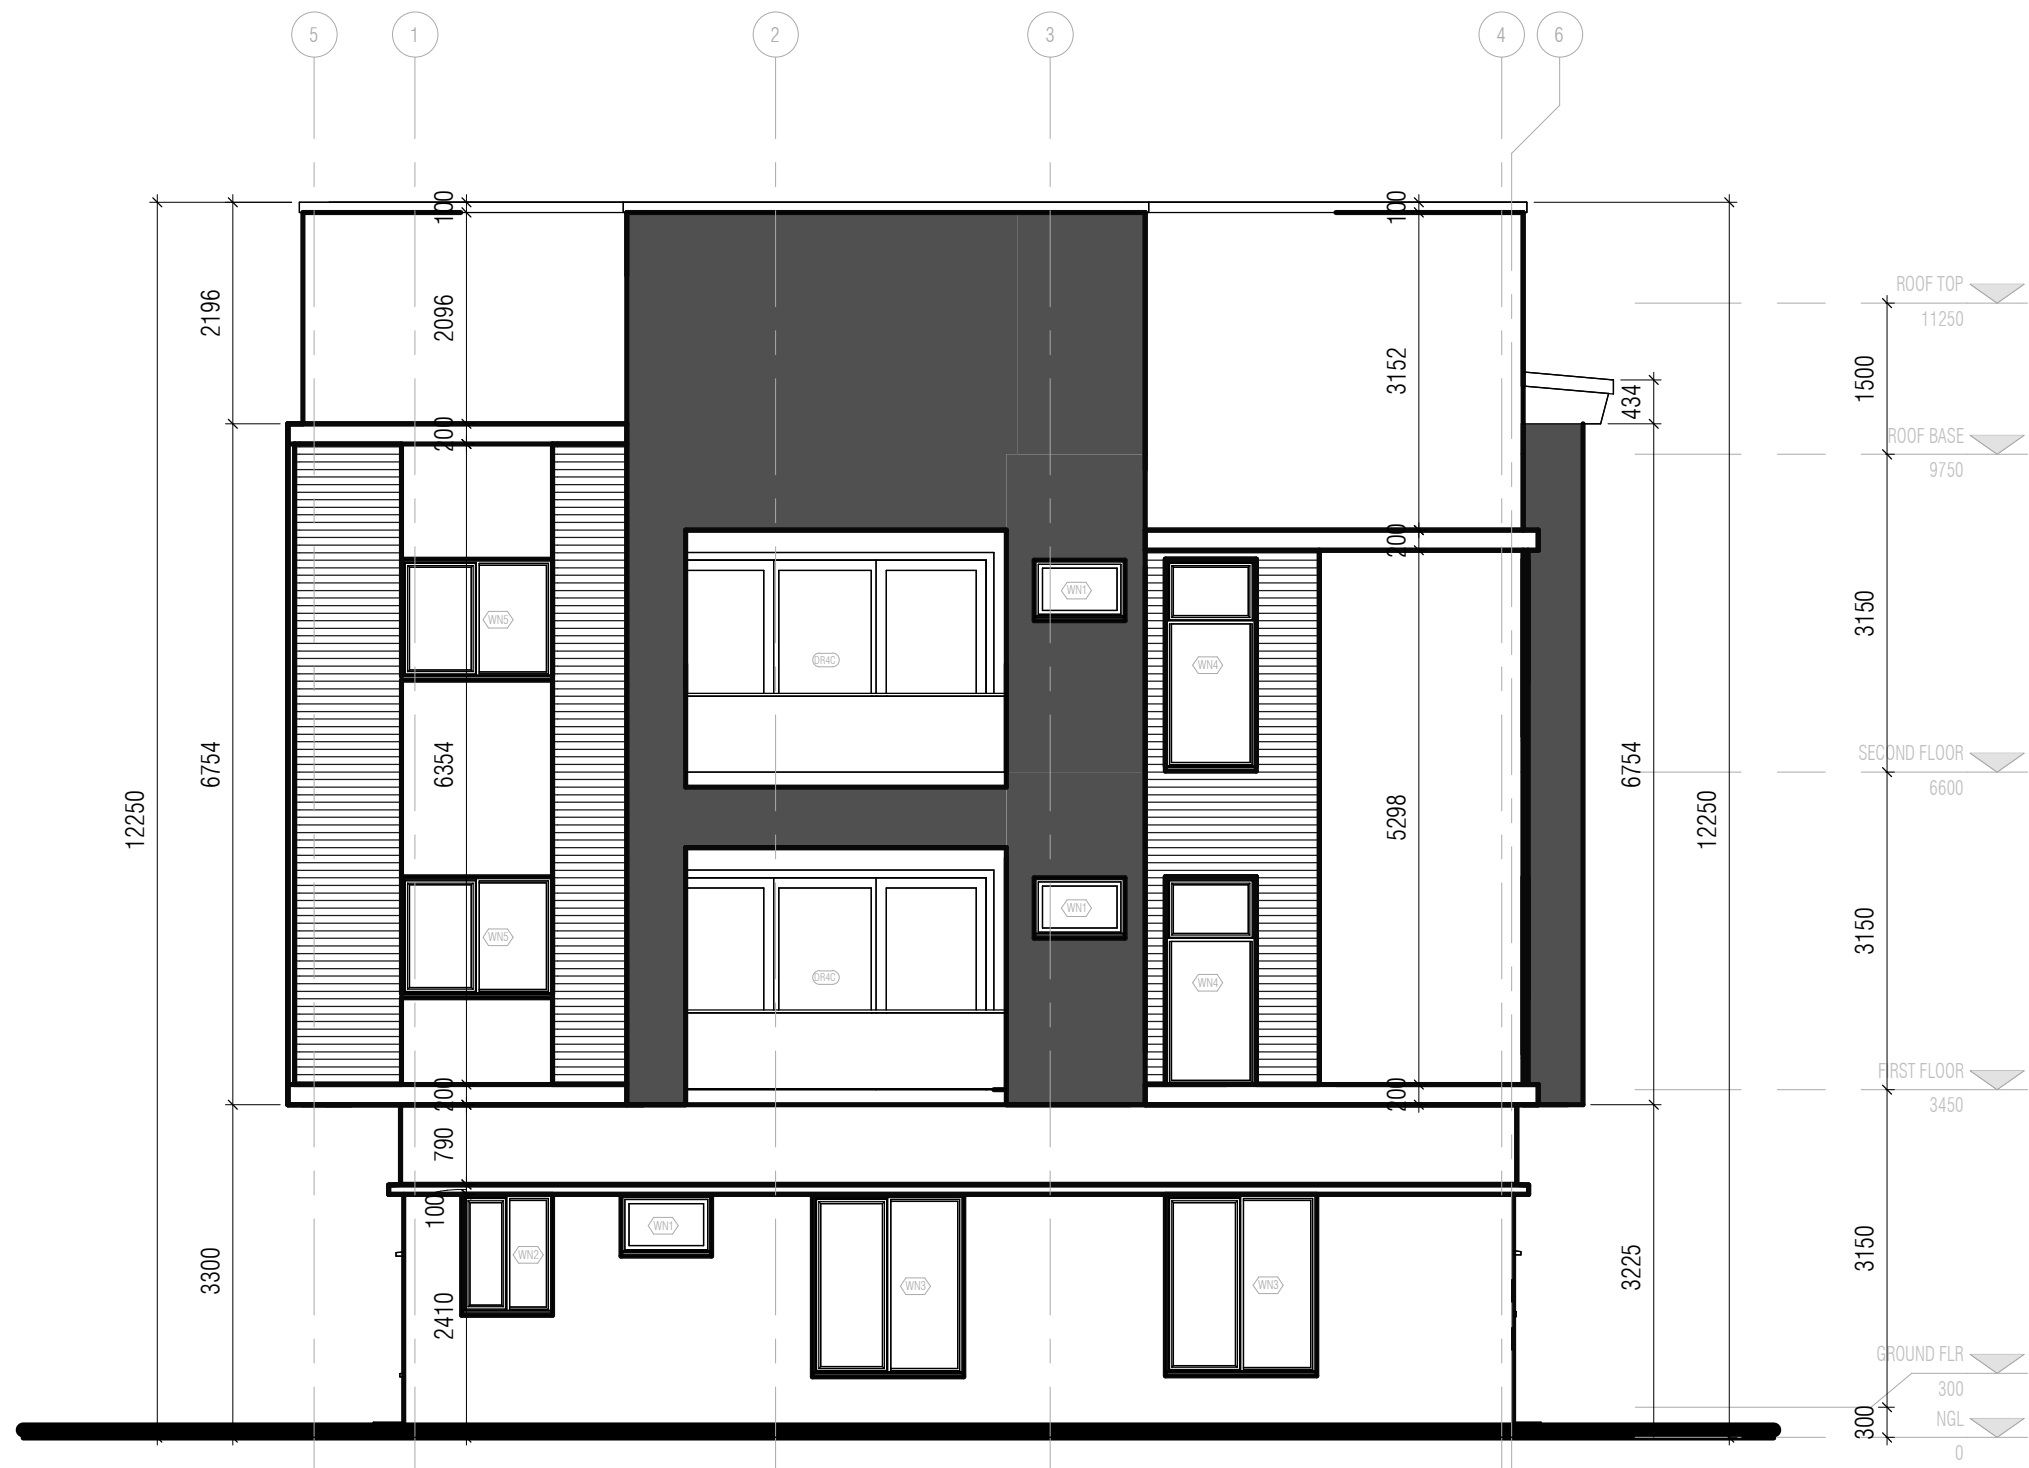



1 Right Elevation
1 : 75





6A, OGUNLEYE STREET, AKOKA, LAGOS.


Project:	RESIDENTIAL DEVELOPMENT	Client:	DARALL HOMES LIMITED	Status:	Approval
Title:	RIGHT ELEVATION	Checked By:	A.H	Date/Rev:	2/18/2026 9:39:21 AM
Scale/Format:	1 : 75	Drawn By:	H.J	Sheet no:	P223

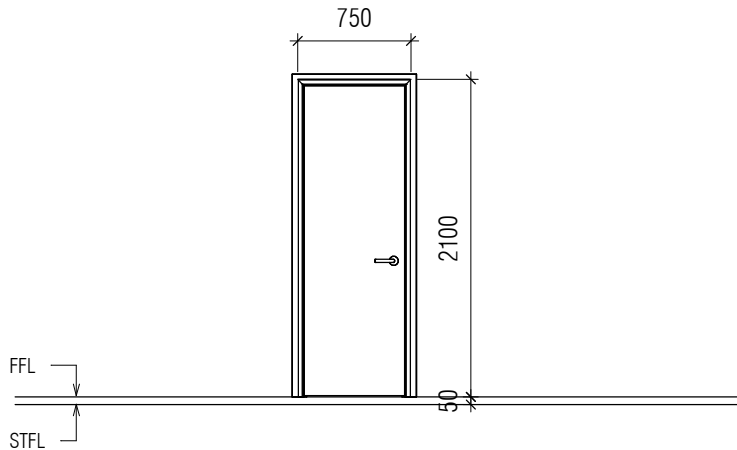
DOOR TYPE		DR1		
				
DIMENSIONS	WIDTH	HEIGHT	QUANTITY	LOCATION
	750	2100	17	GF - VISTR. BATHROOM AND BATHROOMS
DESCRIPTION	INTERNAL SINGLE PANELED WOODEN DOOR 44mm SINGLE LEAF SOLID CORE OUTWARD SWING, NATURAL WOOD FINISH FLUSH DOOR WITH ALL ACCESSORIES i.e LOCKS AND HINGES, DOOR STOPPER TO BE BRUSHED CHROME PLATED OR STAINLESS FINISH INSTALLED TO MANUFACTURER'S DEATILS AND ARCHITECT'S APPROVAL			
SWING	L			
	R			

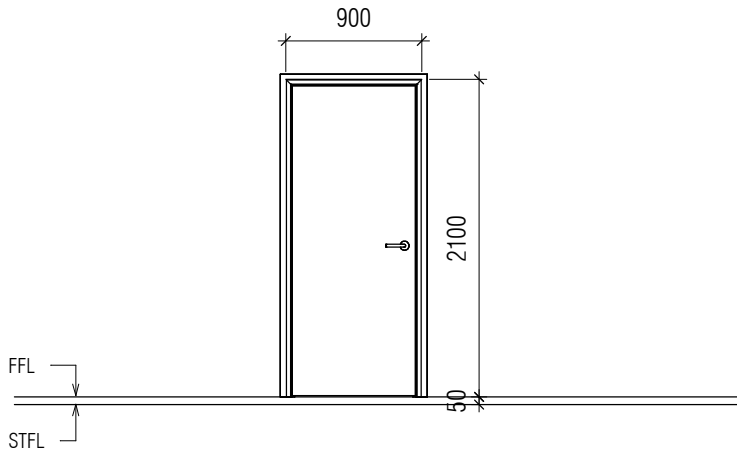DOOR TYPE		DR2		
				
DIMENSIONS	WIDTH	HEIGHT	QUANTITY	LOCATION
	900	2100	22	GF - LIVING AREA, BEDROOMS AND KITCHENS
DESCRIPTION	INTERNAL SINGLE PANELED WOODEN DOOR 44mm SINGLE LEAF SOLID CORE OUTWARD SWING, NATURAL WOOD FINISH FLUSH DOOR WITH ALL ACCESSORIES i.e LOCKS AND HINGES, DOOR STOPPER TO BE BRUSHED CHROME PLATED OR STAINLESS FINISH INSTALLED TO MANUFACTURER'S DEATILS AND ARCHITECT'S APPROVAL			
SWING	L			
	R			

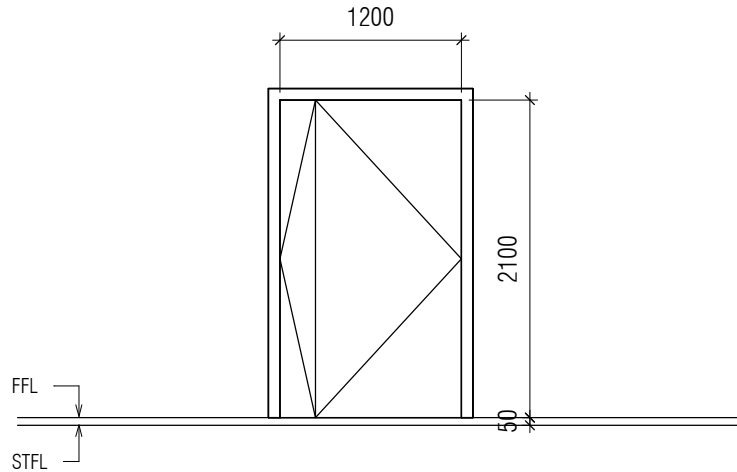DOOR TYPE	DR3			
				
DIMENSIONS	WIDTH	HEIGHT	QUANTITY	LOCATION
	1200	2100	1	GF,FF,PF - BEDROOMS,LOOBY
DESCRIPTION	INTERNAL SINGLE PANELED WOODEN DOOR 44mm SINGLE LEAF SOLID CORE OUTWARD SWING, NATURAL WOOD FINISH FLUSH DOOR WITH ALL ACCESSORIES i.e LOCKS AND HINGES, DOOR STOPPER TO BE BRUSHED CHROME PLATED OR STAINLESS FINISH INSTALLED TO MANUFACTURER'S DEATILS AND ARCHITECT'S APPROVAL			
SWING	L			
	R			

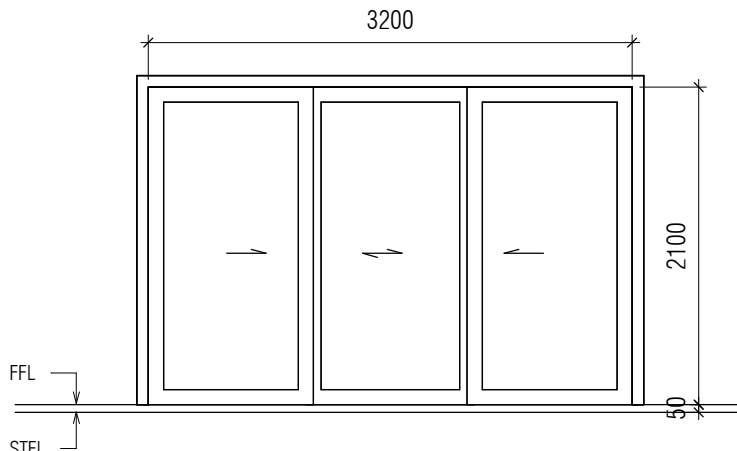DOOR TYPE	DR4A			
				
DIMENSIONS	WIDTH	HEIGHT	QUANTITY	LOCATION
	3200	2100	1	LIVING AREA
DESCRIPTION	THREE PANEL GLAZED SLIDING DOOR. 25mm TOUGHENED GLADED THREEPANEL SLIDING DOOR i.e LOCKS AND HINGES, DOOR STOPPER TO BE BRUSHED CHROME PLATED OR STAINLESS FINISH INSTALLED TO MANUFACTURER'S DEATILS AND ARCHITECT'S APPROVAL			
SWING	L			
	R			

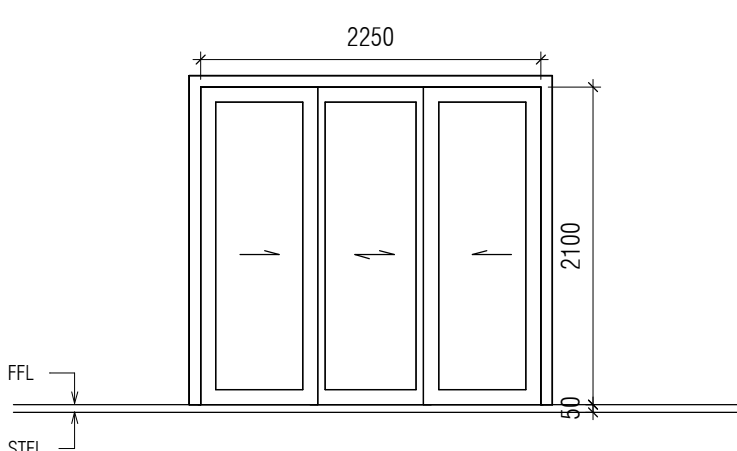DOOR TYPE	DR4B			
				
DIMENSIONS	WIDTH	HEIGHT	QUANTITY	LOCATION
	2250	2100	1	LIVING AREA
DESCRIPTION	THREE PANEL GLAZED SLIDING DOOR. 25mm TOUGHENED GLADED THREEPANEL SLIDING DOOR i.e LOCKS AND HINGES, DOOR STOPPER TO BE BRUSHED CHROME PLATED OR STAINLESS FINISH INSTALLED TO MANUFACTURER'S DEATILS AND ARCHITECT'S APPROVAL			
SWING	L			
	R			

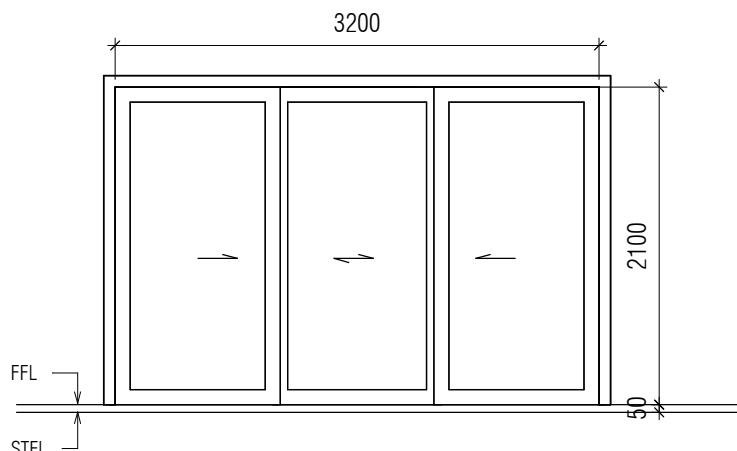DOOR TYPE	DR4C			
				
DIMENSIONS	WIDTH	HEIGHT	QUANTITY	LOCATION
	3200	2100	2	LIVING AREA
DESCRIPTION	THREE PANEL GLAZED SLIDING DOOR. 25mm TOUGHENED GLADED THREEPANEL SLIDING DOOR i.e LOCKS AND HINGES, DOOR STOPPER TO BE BRUSHED CHROME PLATED OR STAINLESS FINISH INSTALLED TO MANUFACTURER'S DEATILS AND ARCHITECT'S APPROVAL			
SWING	L			
	R			

DOOR TYPE

DR5

DIMENSIONS	WIDTH	HEIGHT	QUANTITY	LOCATION
	2900	2100	2	LIVING AREA
DESCRIPTION	THREE PANEL GLAZED SLIDING DOOR. 25mm TOUGHENED GLADED THREEPANEL SLIDING DOOR i.e LOCKS AND HINGES, DOOR STOPPER TO BE BRUSHED CHROME PLATED OR STAINLESS FINISH INSTALLED TO MANUFACTURER'S DEATILS AND ARCHITECT'S APPROVAL			
SWING	L			
	R			

APPROVAL COLUMN


WINDOW TYPE		WN1				WINDOW TYPE		WN2				WINDOW TYPE		WN3			
DIMENSIONS	WIDTH	HEIGHT	QUANTITY	LOCATION		DIMENSIONS	WIDTH	HEIGHT	QUANTITY	LOCATION		DIMENSIONS	WIDTH	HEIGHT	QUANTITY	LOCATION	
	900	600	15	BATHROOMS			900	1200	6	KITCHEN			1500	1800	12	BEDROOMS	
DESCRIPTION	ALUMINIUM CASMENT WINDOW W/ 65mm HOLLOW SECTION, WITH PROFILE TYPE; GRAY ANODIZED ALUMINIUM EXTRUSION, MITRED AT JOINT, SINGLE GLAZED OF 12mm, POWDER COATED GREY COLOR OF EXTERNAL AND APPROVED COLOR OF INTERNAL QUALITY, INSTALLED TO MANUFACTURER'S DEATILS AND ARCHITECT'S APPROVAL					DESCRIPTION	ALUMINIUM CASMENT WINDOW W/ 65mm HOLLOW SECTION, WITH PROFILE TYPE; GRAY ANODIZED ALUMINIUM EXTRUSION, MITRED AT JOINT, SINGLE GLAZED OF 12mm, POWDER COATED GREY COLOR OF EXTERNAL AND APPROVED COLOR OF INTERNAL QUALITY, INSTALLED TO MANUFACTURER'S DEATILS AND ARCHITECT'S APPROVAL					DESCRIPTION	ALUMINIUM CASMENT WINDOW W/ 65mm HOLLOW SECTION, WITH PROFILE TYPE; GRAY ANODIZED ALUMINIUM EXTRUSION, MITRED AT JOINT, SINGLE GLAZED OF 12mm, POWDER COATED GREY COLOR OF EXTERNAL AND APPROVED COLOR OF INTERNAL QUALITY, INSTALLED TO MANUFACTURER'S DEATILS AND ARCHITECT'S APPROVAL				
SWING	L					SWING	L					SWING	L				
	R						R						R				

WINDOW TYPE		WN4			WINDOW TYPE		WN4A			WINDOW TYPE		WN4B		
DIMENSIONS	WIDTH	HEIGHT	QUANTITY	LOCATION	DIMENSIONS	WIDTH	HEIGHT	QUANTITY	LOCATION	DIMENSIONS	WIDTH	HEIGHT	QUANTITY	LOCATION
	900	2100	3	BEDROOM		600	2100	1	STUDIO APARTMENT		750	2100	2	BEDROOM
DESCRIPTION	ALUMINIUM CASMENT WINDOW W/ 65mm HOLLOW SECTION, 600X900MM OPENABLE PANEL, WITH PROFILE TYPE; GRAY ANODIZED ALUMINIUM EXTRUSION, MITRED AT JOINT, SINGLE GLAZED OF 12mm, POWDER COATED GREY COLOR OF EXTERNAL AND APPROVED COLOR OF INTERNAL QUALITY, INSTALLED TO MANUFACTURER'S DEATILS AND ARCHITECT'S APPROVAL				DESCRIPTION	ALUMINIUM CASMENT WINDOW W/ 65mm HOLLOW SECTION, 600X600MM OPENABLE PANEL, WITH PROFILE TYPE; GRAY ANODIZED ALUMINIUM EXTRUSION, MITRED AT JOINT, SINGLE GLAZED OF 12mm, POWDER COATED GREY COLOR OF EXTERNAL AND APPROVED COLOR OF INTERNAL QUALITY, INSTALLED TO MANUFACTURER'S DEATILS AND ARCHITECT'S APPROVAL				DESCRIPTION	ALUMINIUM CASMENT WINDOW W/ 65mm HOLLOW SECTION, 600X750MM OPENABLE PANEL, WITH PROFILE TYPE; GRAY ANODIZED ALUMINIUM EXTRUSION, MITRED AT JOINT, SINGLE GLAZED OF 12mm, POWDER COATED GREY COLOR OF EXTERNAL AND APPROVED COLOR OF INTERNAL QUALITY, INSTALLED TO MANUFACTURER'S DEATILS AND ARCHITECT'S APPROVAL			
SWING	L				SWING	L				SWING	L			
	R					R					R			



6A, OGUNLEYE STREET, AKOKA, LAGOS.

Project:	RESIDENTIAL DEVELOPMENT	Client:	DARALL HOMES LIMITED	Status:	Approval
Title:	WINDOW SCHEDULE	Checked By:	A.H	Date/Rev:	2/18/2026 9:39:23 AM
Scale/Format:	1 : 50	Drawn By:	Author	Sheet no:	P310

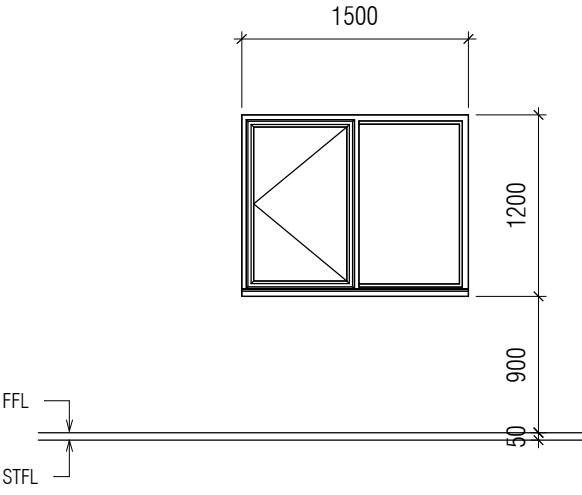WINDOW TYPE	WN5			
				
DIMENSIONS	WIDTH	HEIGHT	QUANTITY	LOCATION
	1500	1200	2	KITCHEN
DESCRIPTION	ALUMINIUM SLIDING WINDOW W/ 65mm HOLLOW SECTION, WITH PROFILE TYPE; GRAY ANODIZED ALUMINIUM EXTRUSION, MITRED AT JOINT, SINGLE GLAZED OF 12mm, POWDER COATED GREY COLOR OF EXTERNAL AND APPROVED COLOR OF INTERNAL QUALITY, INSTALLED TO MANUFACTURER'S DEATILS AND ARCHITECT'S APPROVAL			
SWING	L			
	R			



6A, OGUNLEYE STREET, AKOKA, LAGOS.

Project:	RESIDENTIAL DEVELOPMENT	Client:	DARALL HOMES LIMITED	Status:	Approval
Title:	WINDOW SCHEDULE	Checked By:	A.H	Date/Rev:	2/18/2026 9:39:23 AM
Scale/Format:	1 : 50	Drawn By:	H.J	Sheet no:	P311